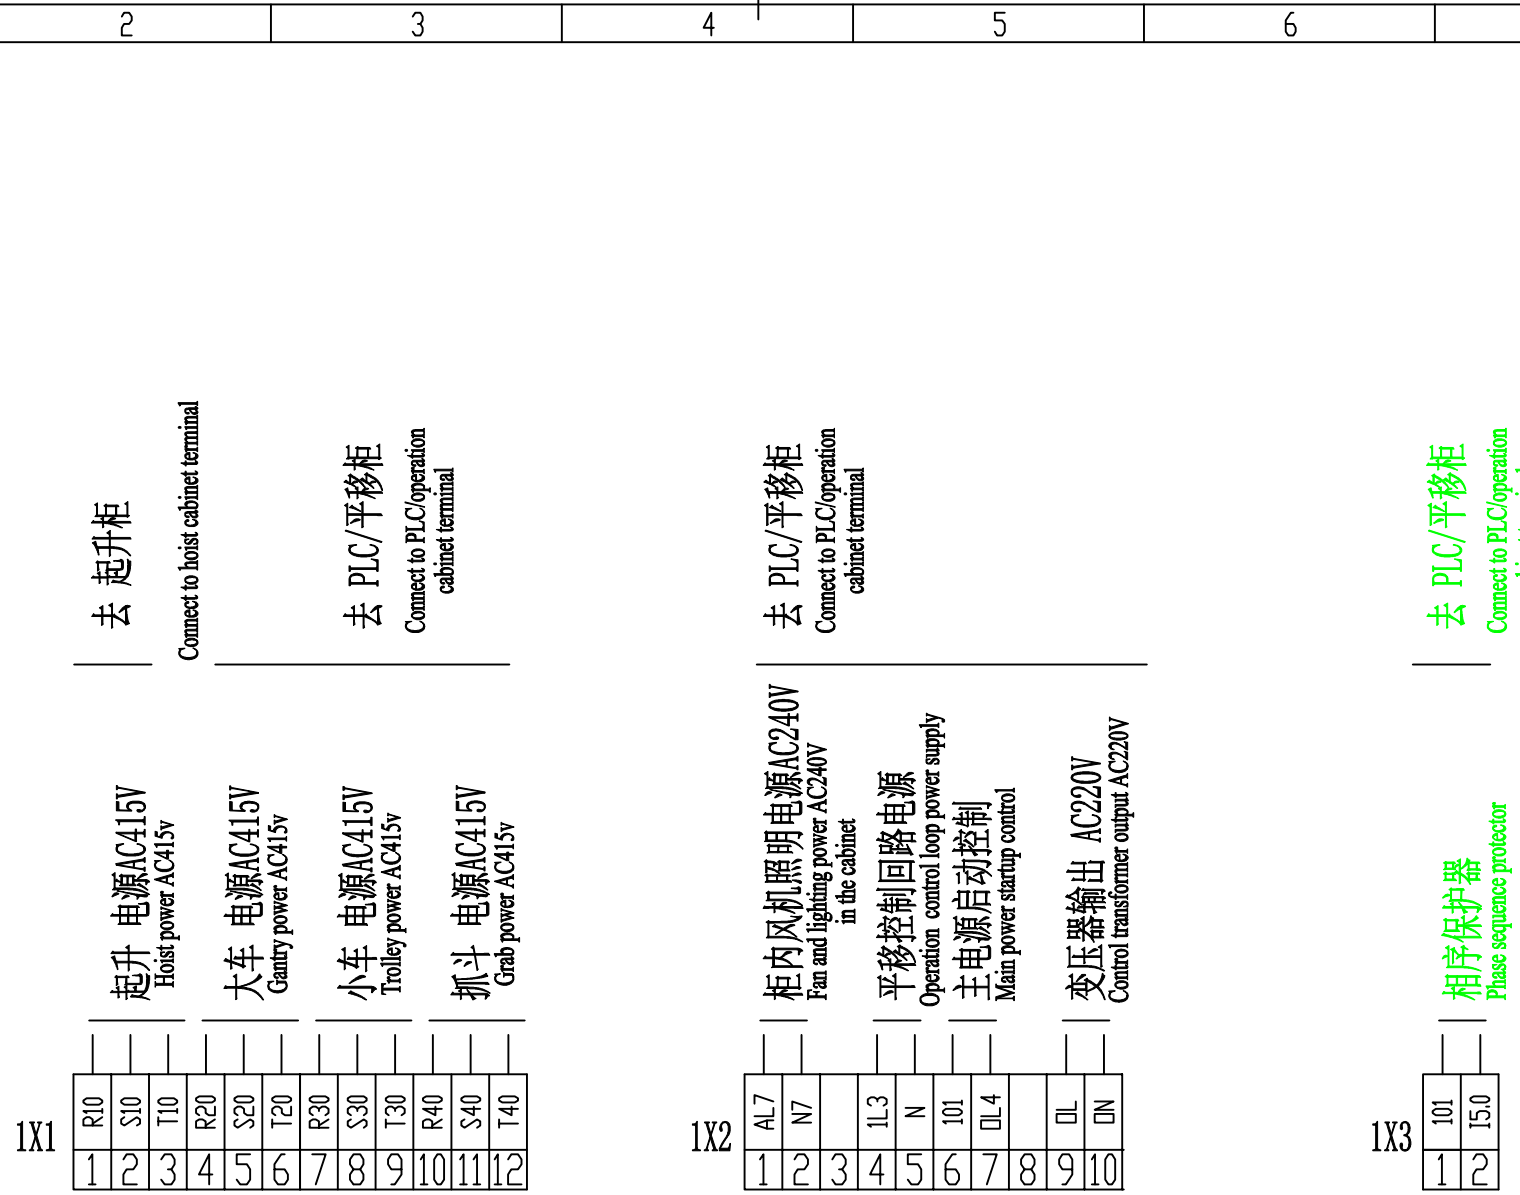

备注：绿色字体是弱电，强电和弱电要用不同端子。
Remark:Green font is low voltage,high and low voltage ia different.

d					设 计 Designed by	孙佳炜 Sun Jiawei		
c					审 查 Reviewed by	董晨 Dong Chen		
b					主管设计 Chief Designer	石振 Shi Zhen		
a								
标记 Mark	处数 Nos.	更改文件号 Changed File No.	签 字 Signature					

项 目 Item	城市生活垃圾焚烧发电厂 垃圾抓斗桥式起重机 Municipal solid waste incineration power plant Waste grab bridge crane	浙江浙起机械有限公司 Zhejiang Zheqi Machinery Co., Ltd.	名 称 Description	电源柜 端子图 Power cabinet terminal
	18t 37.1m A8	地址：浙江省金华市金东区岭下朱工业区 Add: Lingxiazhu Industrial Zone, Jindong District, Jinhua City, Zhejiang Province	质 量 Quality / 比 例 Scale	

图 号 DWG No.	QZL/0101-A		
下页 Next page		本页 This page	1
页 数 Sheet	3	页 次 Sheet of	1

图纸总张次 Total sheet: **

借(通)用件登记 Borrowed (General) Parts Registration

描 Traced by 图

描 Checked by 校

旧 底 图 总 号 General No. of Old Traced Drawing

底 图 总 号 Base Drawing Total No.

签 Signature 字

日 Date 期