
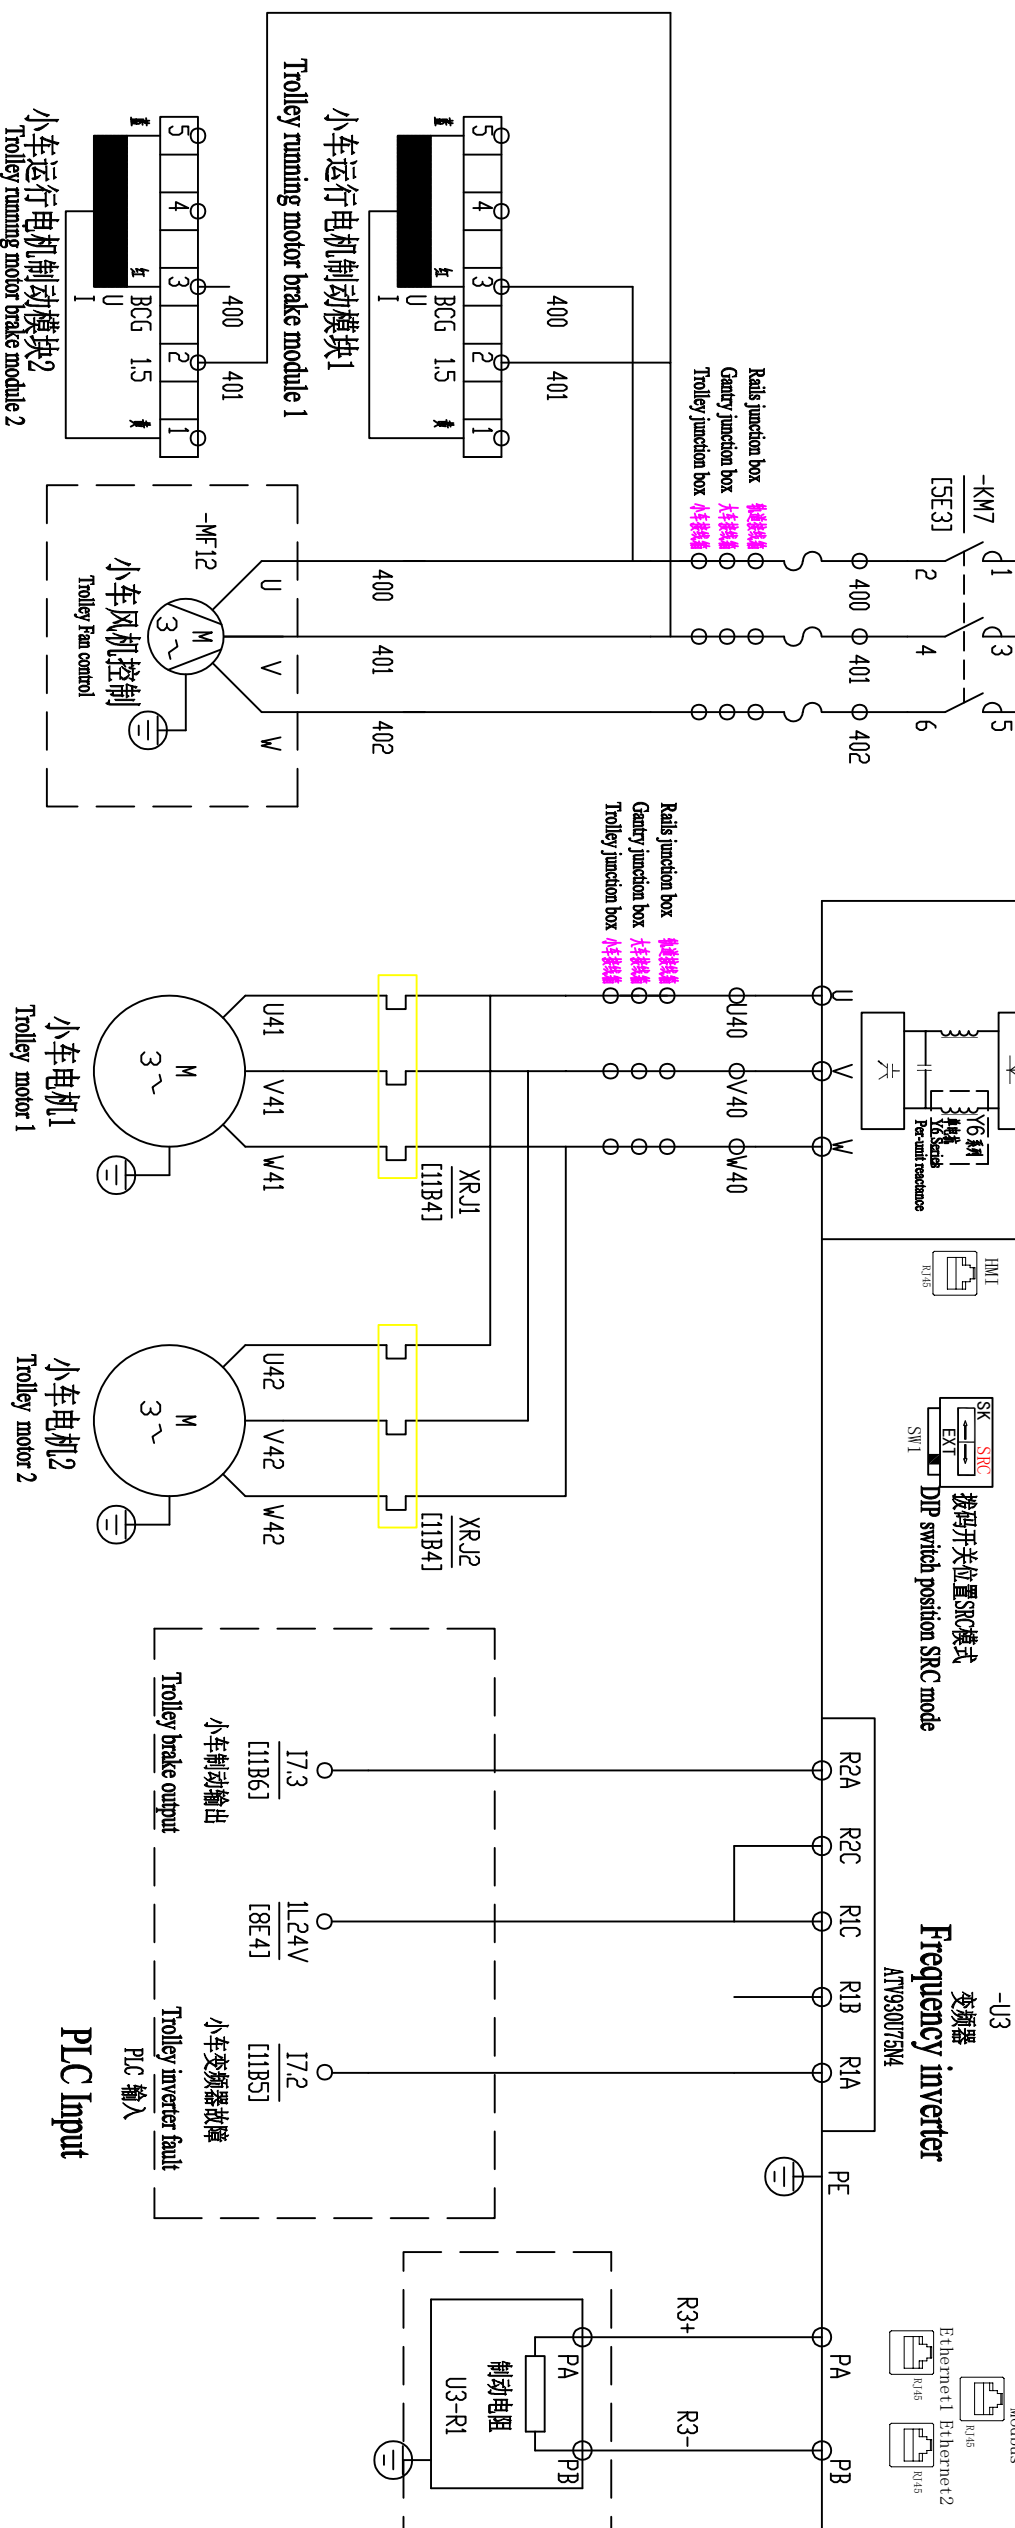
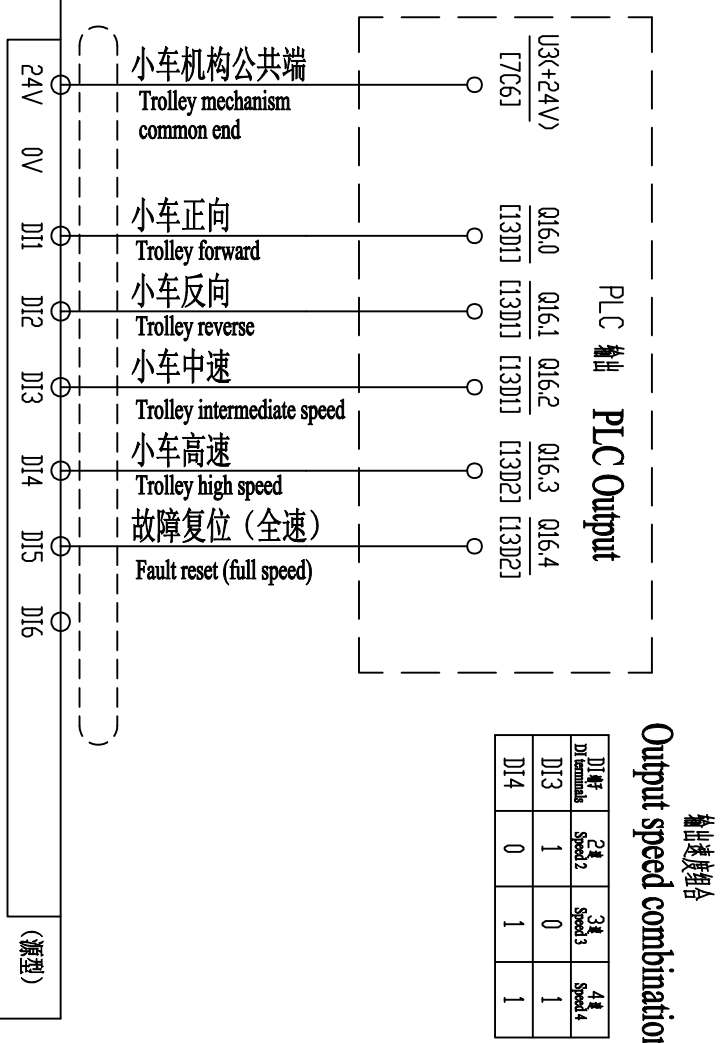


0								
1								
2								
3								
4								
5								
6								
7								
8								
9								

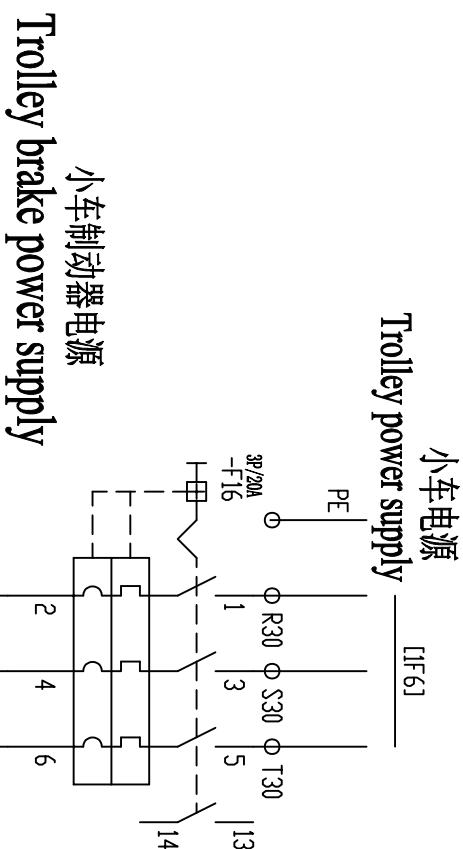

浙江浙起机械有限公司 Zhejiang Zheqi Machinery Co., Ltd.					
地址：浙江省金华市金东区岭下朱工业区 Add: Lingxiayin Industrial Zone, Jindong District, Jinhu City, Zhejiang Province					
名称 Description		小车运行机构 Trolley running mechanism		图号 DWG No.	页次 QZL / 0101 -4
数量 Quantity		比例 Scale		页码 Sheet page	共几页 Total page
				5	4
项 目 Municipal solid waste incineration power plant Waste grab bridge crane					
18t		37.1m A8			
Mark Nos. Checked The No. Signature					
a	设计 Designed by	孔生巧 Jun Shengqiao			
c	审核 Reviewed by	王雪平 Ding Chen			
b	主审 Chief Designer	王雪平 Shi Zhen			
d					