
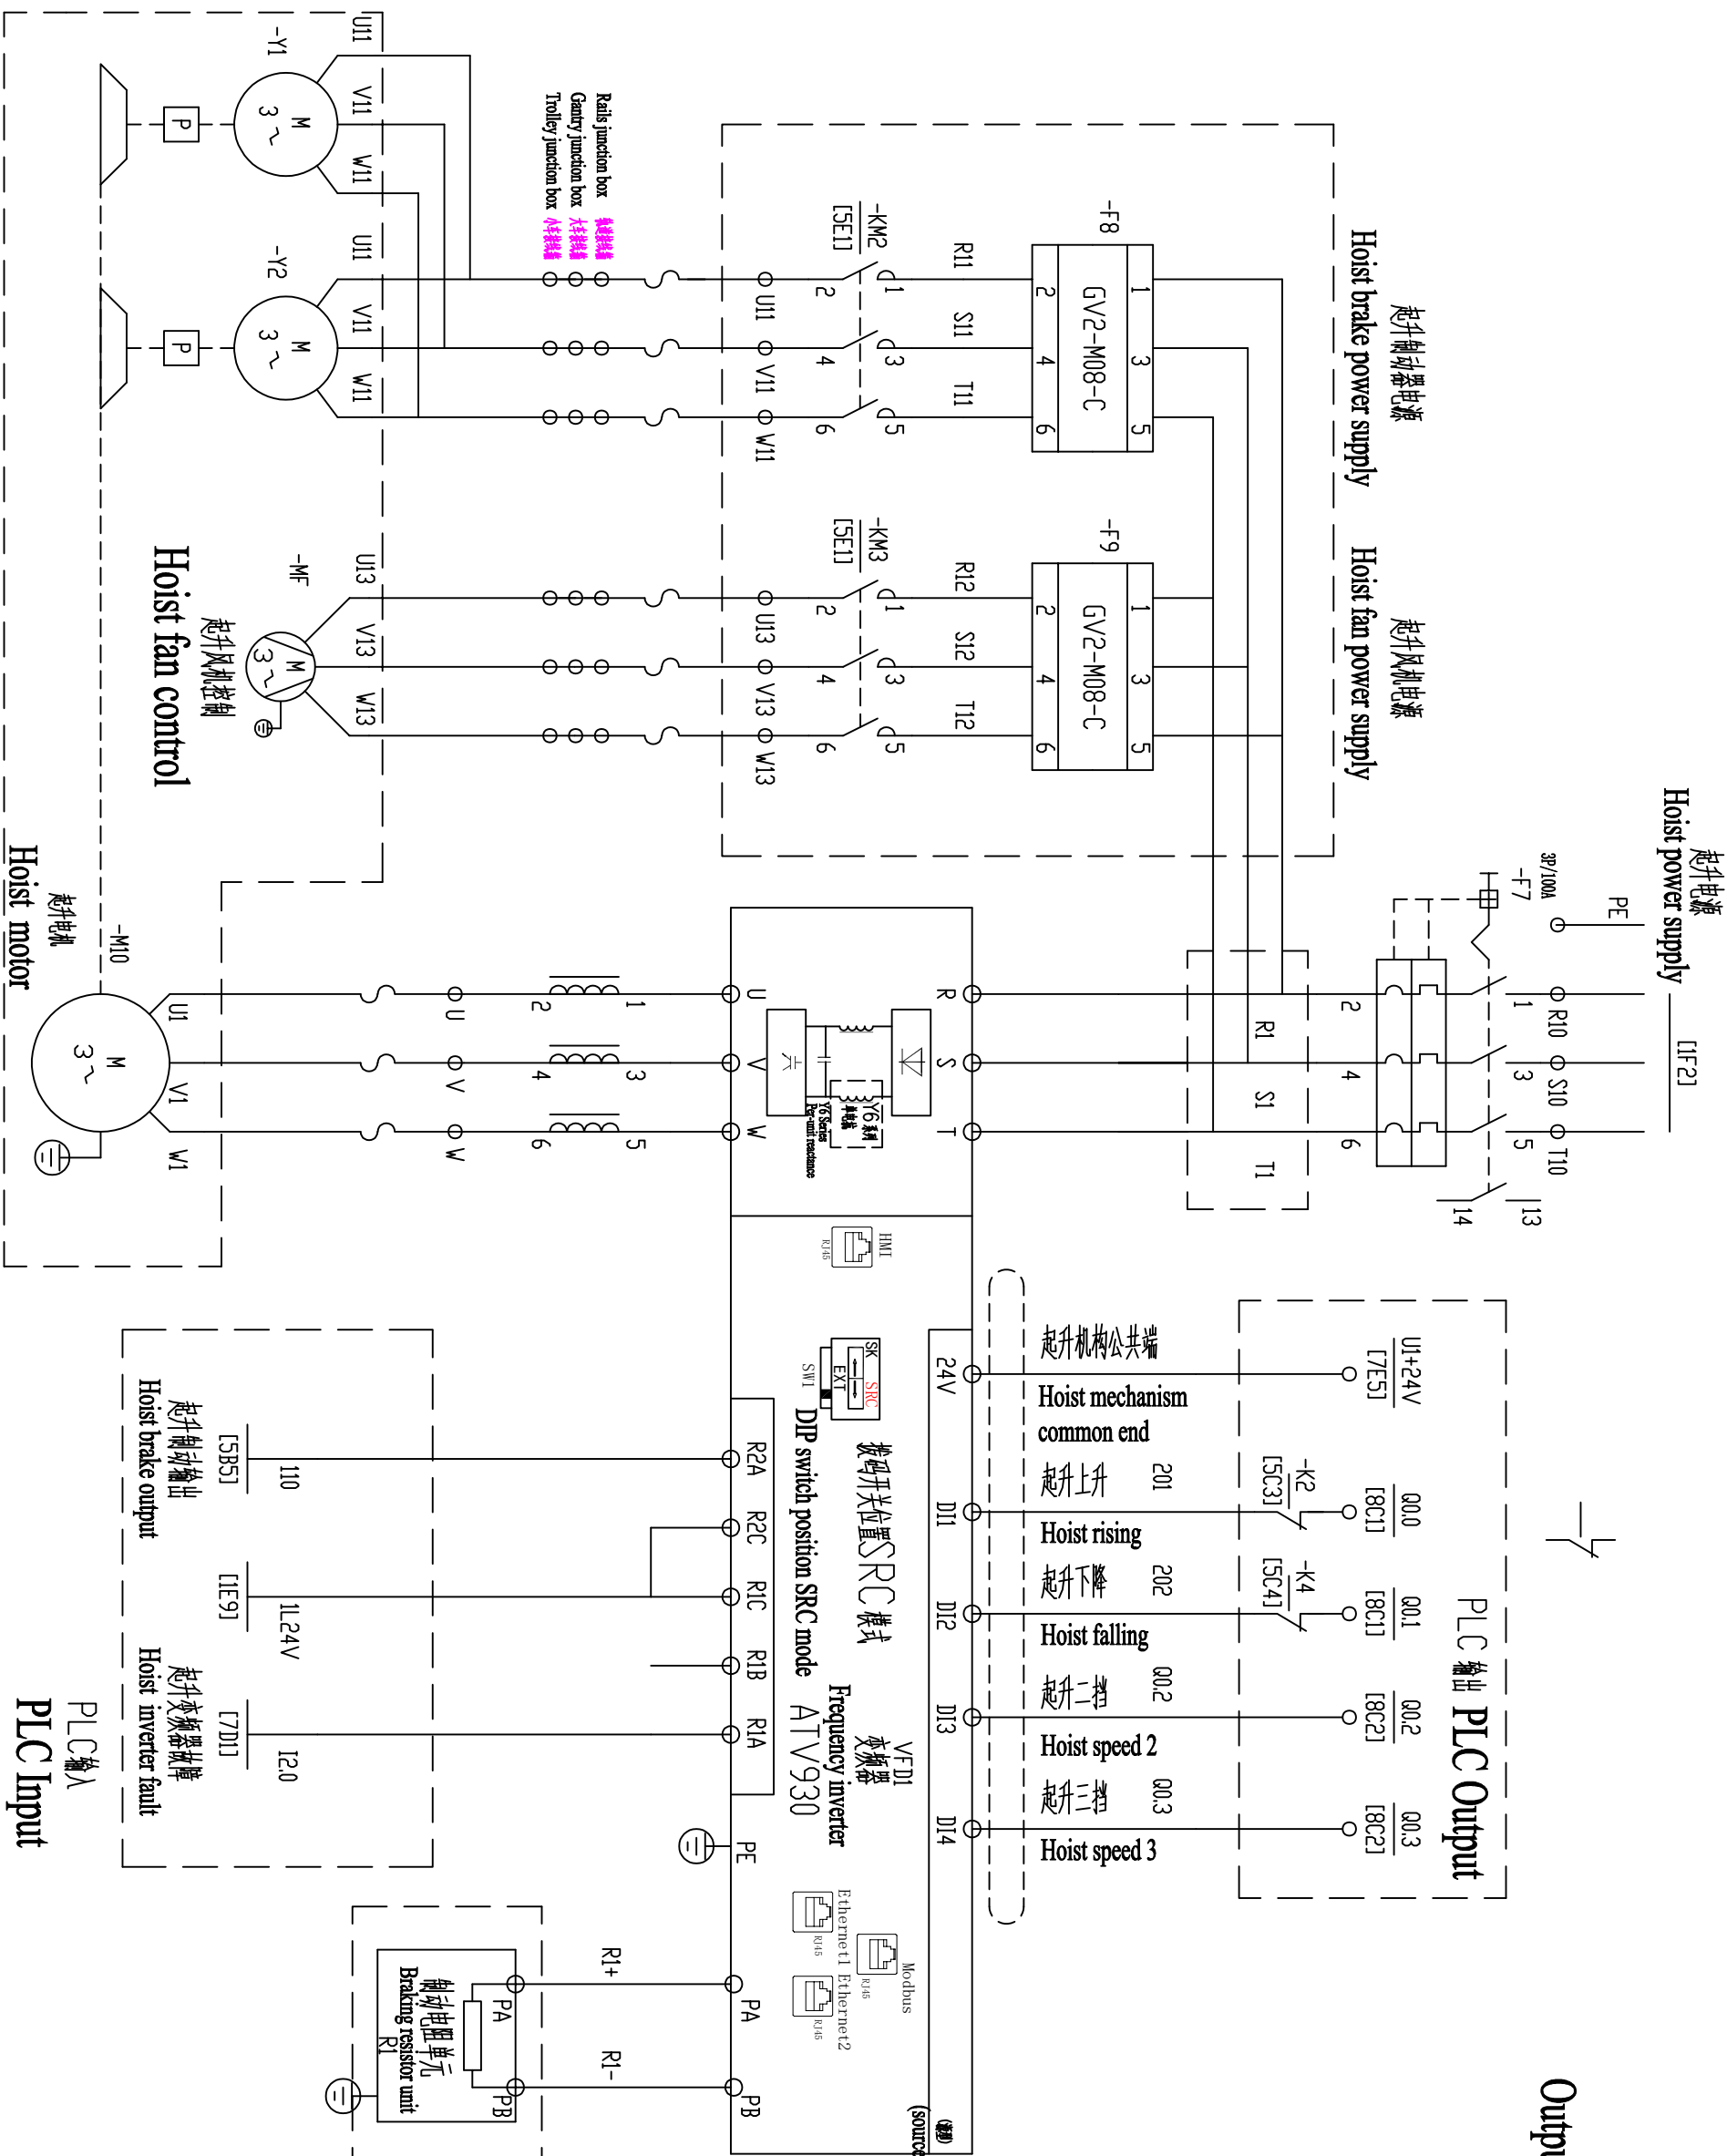
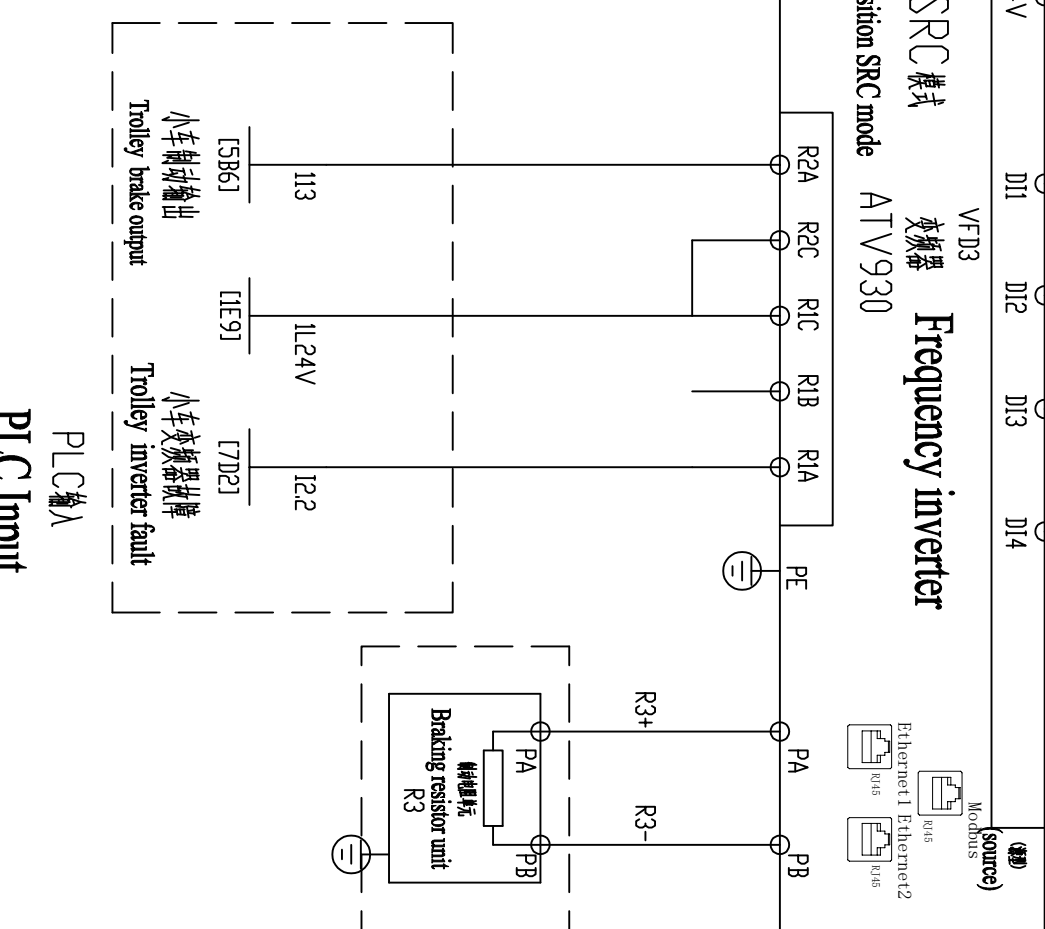
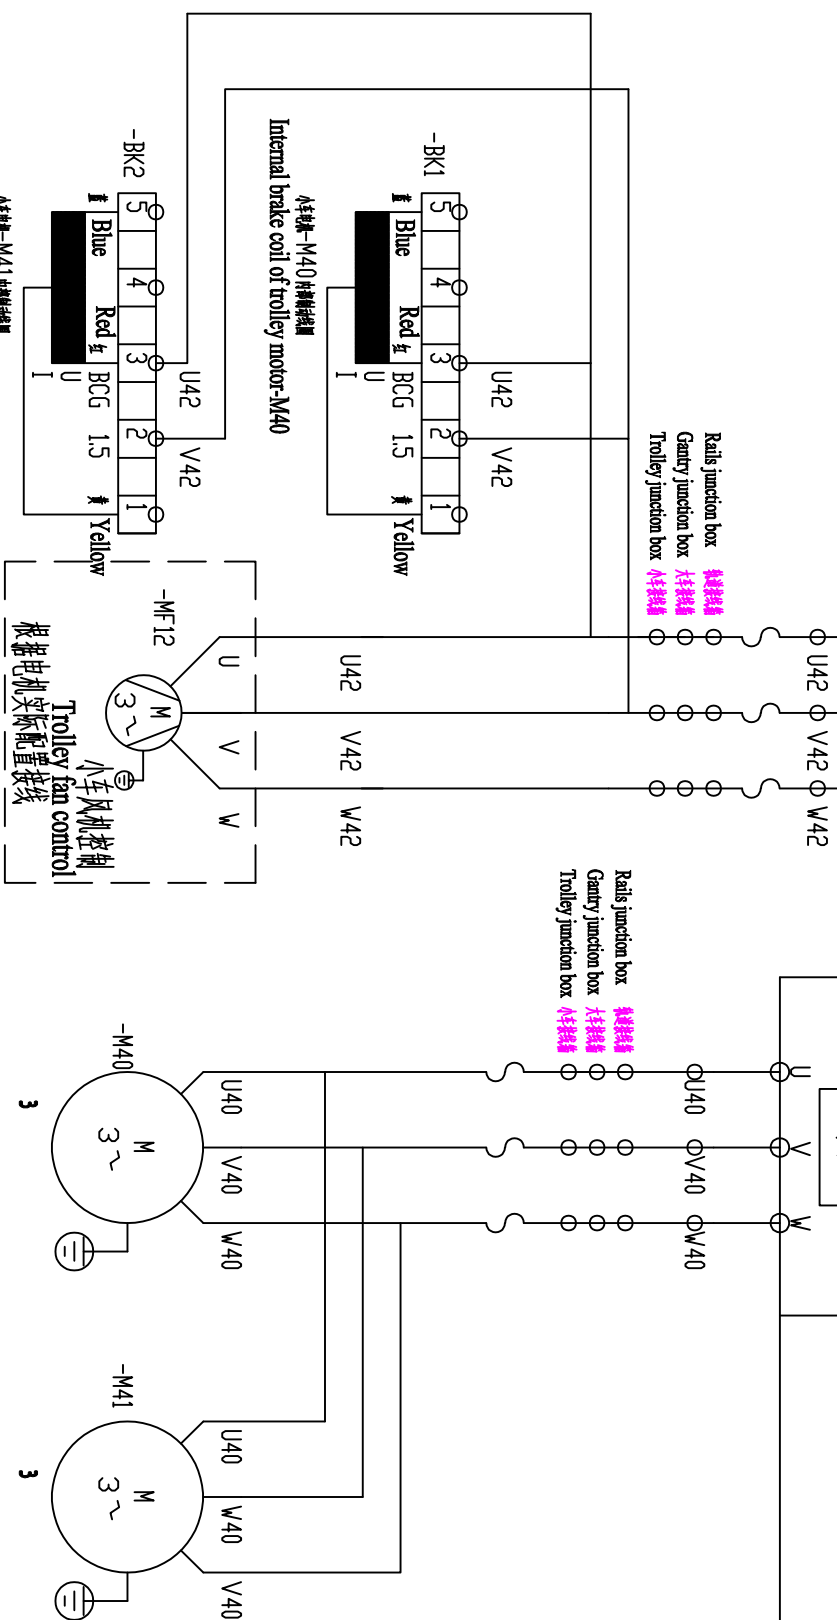
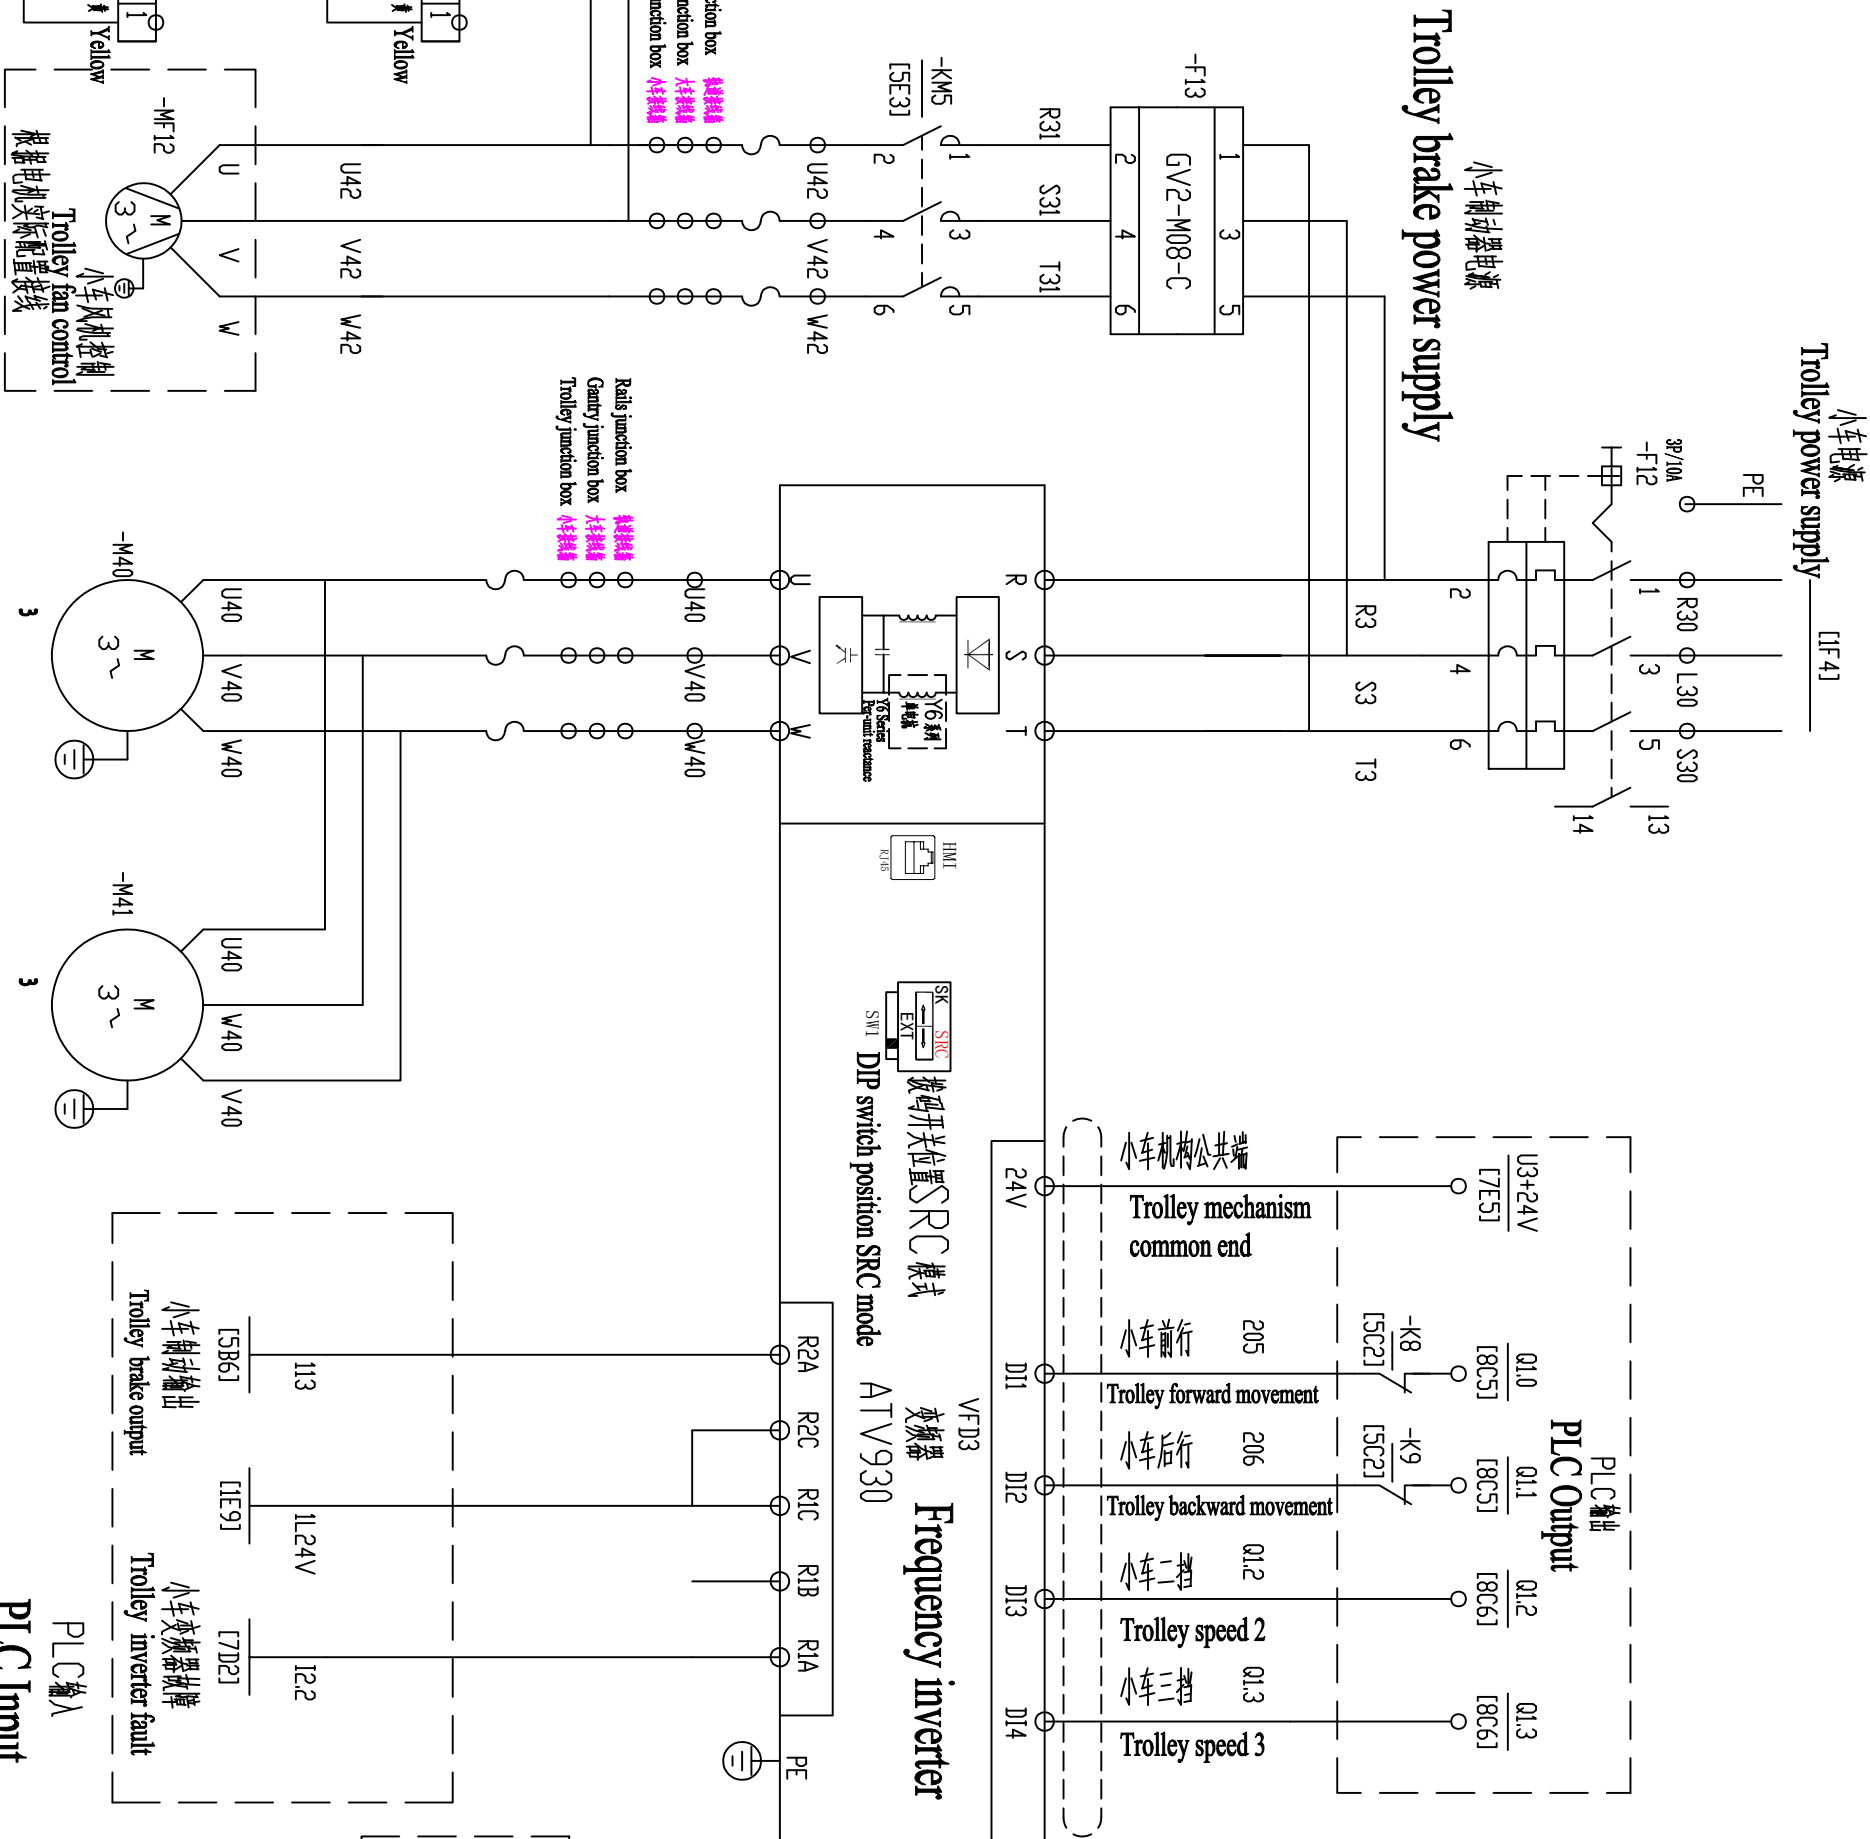
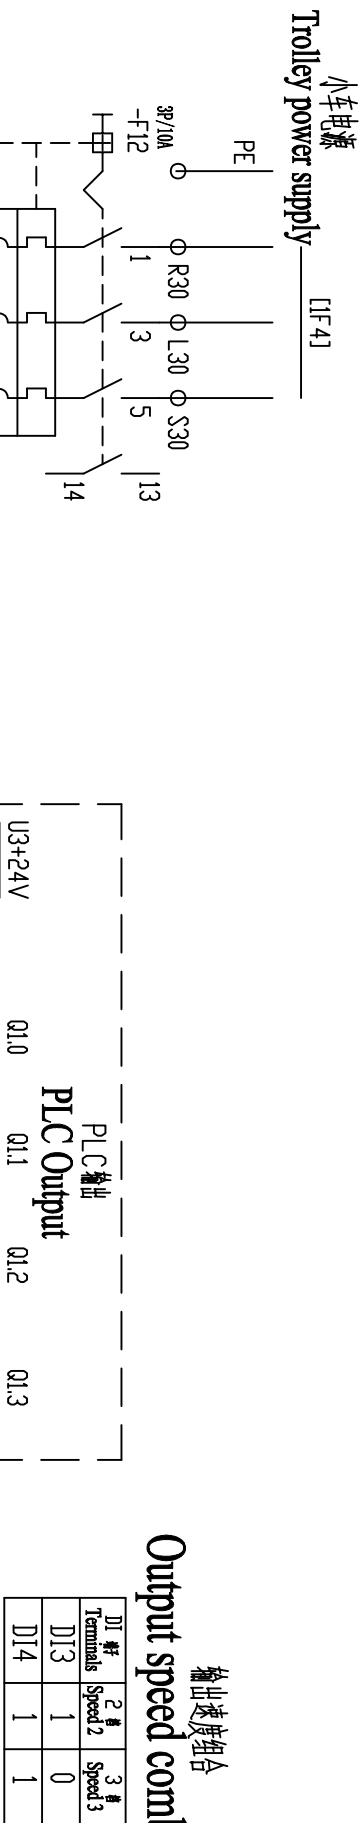
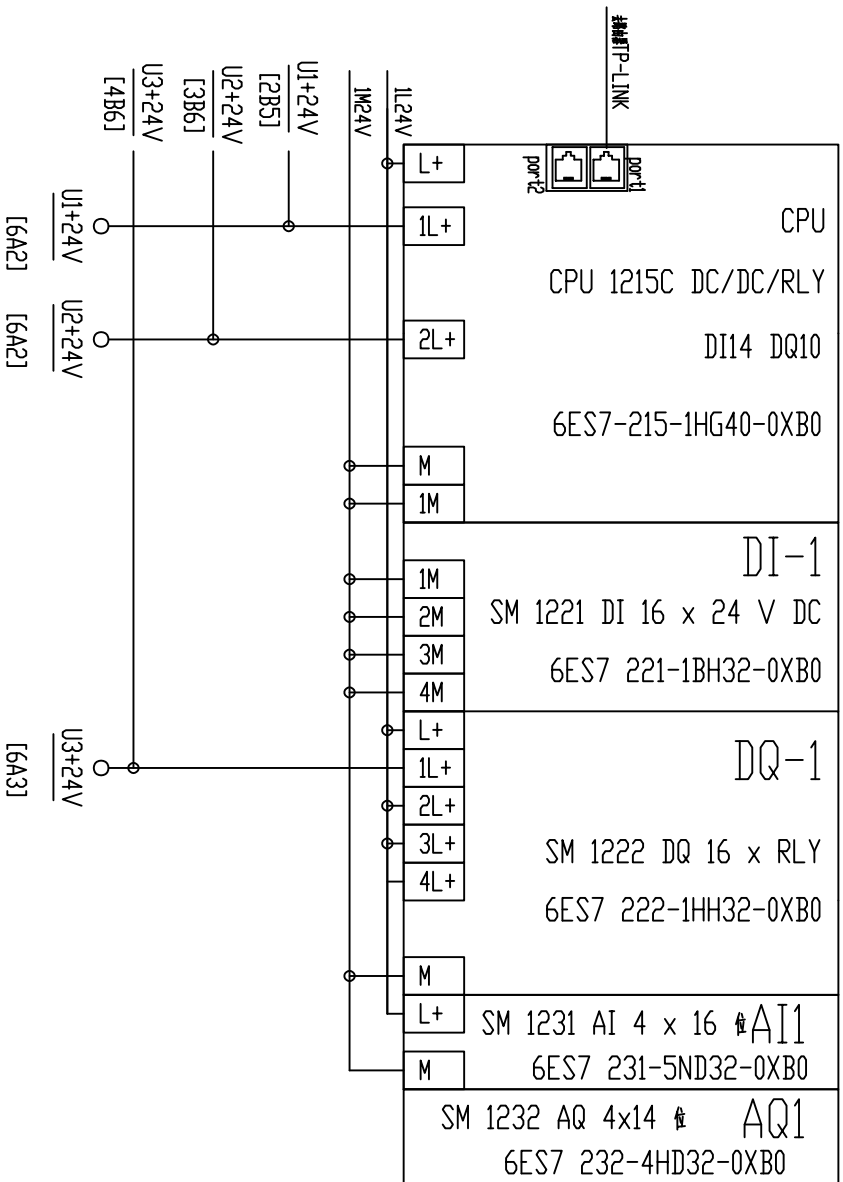


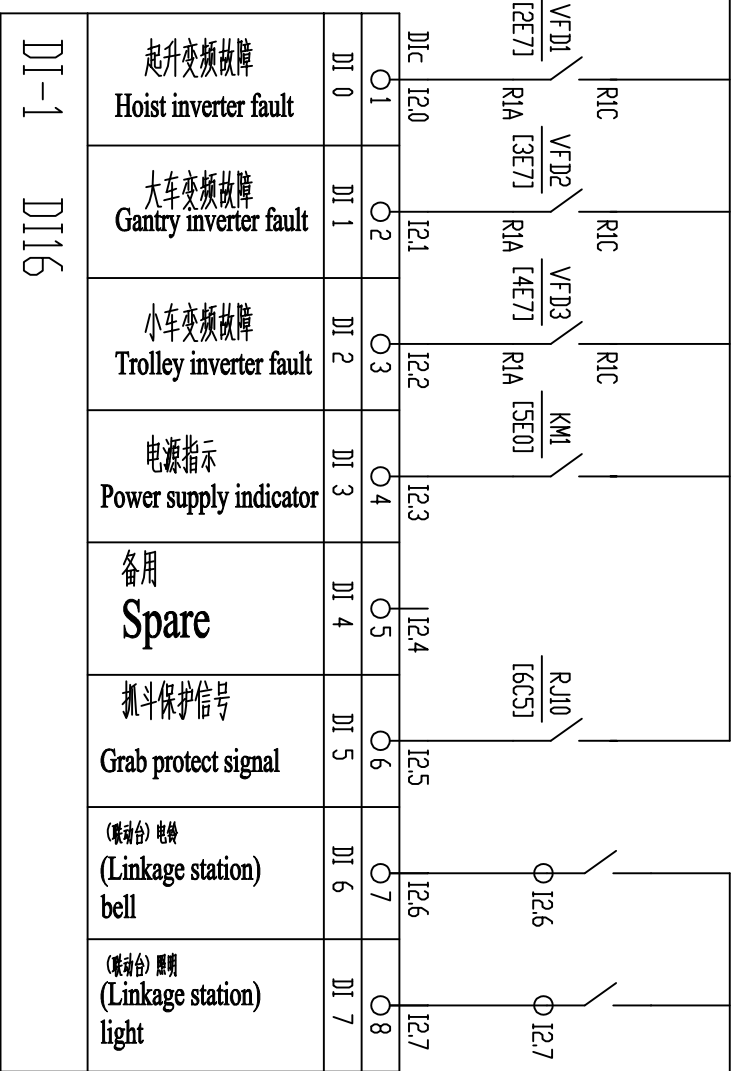

DI 籽 Terminals	2 齒 Speed 2	3 齒 Speed 3
DI3	1	0
DI4	1	1

[illegible]

[illegible]

[illegible][illegible]

0								
1								
2								
3								
4								
5								
6								
7								
8								
9								

IX1		1	U30			
		2	V30			
		3	W30			
		4	R2+			
		5	R2-			
		6	U40			
		7	V40			
		8	W40			
		9	R3+			
		10	R3-			
IX3		1	1JR11			
		2	1JR12			
		3				
		4	1JR21			
		5	1JR22			
		6				
		7	1JR31			
		8	1JR32			
		9				
		10				
IX11		1	RL1			
		2	RN1			
		3				
		4	621			
		5	620			
		6	622			
		7	624			
		8	625			
		9	626			
		10	627			
IX13		1	607			
		2	608			
		3	Q0.0			
		4	Q0.1			
		5	Q0.2			
		6	Q0.4			
		7	Q0.5			
		8	Q0.6			
		9	Q2.0			
		10	Q2.1			
		11	Q2.2			
		12	Q3.1			
		13	Q3.2			

IX1	1	U30			
	2	V30			
	3	W30			大车电机 Gantry motor 1-2
	4	R2+			
	5	R2-			大车制动电阻 Gantry brake
	6	U40			
	7	V40			小车电机 Trolley motor 1-2
	8	W40			
	9	R3+			
	10	R3-			小车制动电阻 Trolley brake
IX3	1	1JR11			起升电机加热器 Hoist motor heater
	2	1JR12			
	3				
	4	1JR21			大车电机加热器 Gantry motor heater
	5	1JR22			
	6				
	7	1JR31			小车电机加热器 Trolley motor heater
	8	1JR32			
	9				
	10				

遙控器控制電源	1	RL1	
Remote control power	2	RN1	
	3		
	4	621	备用
	5	620	Spare
起吊限位	6	622	
Hoist limit switch	7	624	
	8	625	大車限位
Gantry limit switch	9	626	
	10	627	小車限位
Trolley limit switch			

1X13		
1	607	
2	608	
3	Q0.0	
4	Q0.1	
5	Q0.2	
6	Q0.4	
7	Q0.5	
8	Q0.6	
9	Q2.0	
10	Q2.1	
11	Q2.2	
12	Q3.1	
13	Q3.2	
14	Q3.7	
15	U2+24V	
16	U3+24V	

[illegible]

1X2	
1	U11
2	V11
3	W11
4	U13
5	V13
6	W13

IX14	
1	1L 24V-1
2	1L 24V-1
3	1L 24V-1
4	1L 24V-1
5	1L 24V-1
6	1L 24V-2
7	1L 24V-2
8	1L 24V-2
9	1L 24V-2
10	1L 24V-2

[illegible]

1	U11	起升机构
2	V11	起升机构
3	W11	起升机构
4	U13	起升机构
5	V13	起升机构
6	W13	起升机构
7	U32	起升机构
8	V32	起升机构
9	W32	起升机构
10	U42	起升机构
11	V42	起升机构
12	W42	起升机构
13	U11	起升机构

13	LL1		照明 Light
14	NL1		
15	DL1		电铃 Bell
16	DN1		
17	Y1		集斗开闭信号 Grab open and close signal
18	Y2		
19	DN1		
20	备用		

11	10.7		接联动台 To Linkage station
12	11.0		
13	11.1		
14	11.2		
15	11.3		
16	11.4		
17	11.5		
18	12.6		
19	12.7		
20			

IX15			联动台控制 Linkage station control
1	1L24V		
2	1L24V		
3	1L24V		
4	1L24V		
5	1L24V		DC24V
6	1M24V		
7	1M24V		
8	1M24V		
9	1M24V		

1X2	1	U11		
	2	V11		
	3	W11		起升电机 Hoist fan
	4	U13		
	5	V13		
	6	W13		起升制动器 Hoist brake
	7	U32		
	8	V32		
	9	W32		大车制动器 Gantry brake
	10	U42		
	11	V42		小车制动器 Trolley brake
	12	W42		
	13	LL1		
	14	NL1		照明 Light
	15	DL1		
	16	DN1		电铃 Bell
	17	Y1		
	18	Y2		抓斗开闭信号 Grab open and close signal
	19	DN1		
	20	备用		

IX12	1	600	
	2	603	
	3	605	
	4	10.0	
	5	10.1	
	6	10.2	
	7	10.3	
	8	10.4	
	9	10.5	
	10	10.6	
	11	10.7	
	12	11.0	
	13	11.1	
	14	11.2	
	15	11.3	
	16	11.4	
	17	11.5	
	18	12.6	
	19	12.7	
	20		
	21		

1	1L24V		联站合控制 Linkage station control
2	1L24V		
3	1L24V		
4	1L24V		
5	1L24V		
6	1M24V		
7	1M24V		DC24V
8	1M24V		
9	1M24V		
10	1M24V		

		E0			
		21			

		610		1M24V	
--	--	-----	--	-------	--

		Z00Z/0104-9	
		This page 9	

名称 Description	柜内端子 Cabinet terminal		图号 DWG No.	ZQQZ/0104-9 This page 9			
	质量 Quality	比例 Scale		数量 = 01	张数 9	尺寸 10 毫米	张数 9
				Sheet of			