

Linkage Panel


Analog input module

联动台

模拟量输入模块

无线称重仪表ZQ161RF

Wireless loadcell instrument ZQ161RF

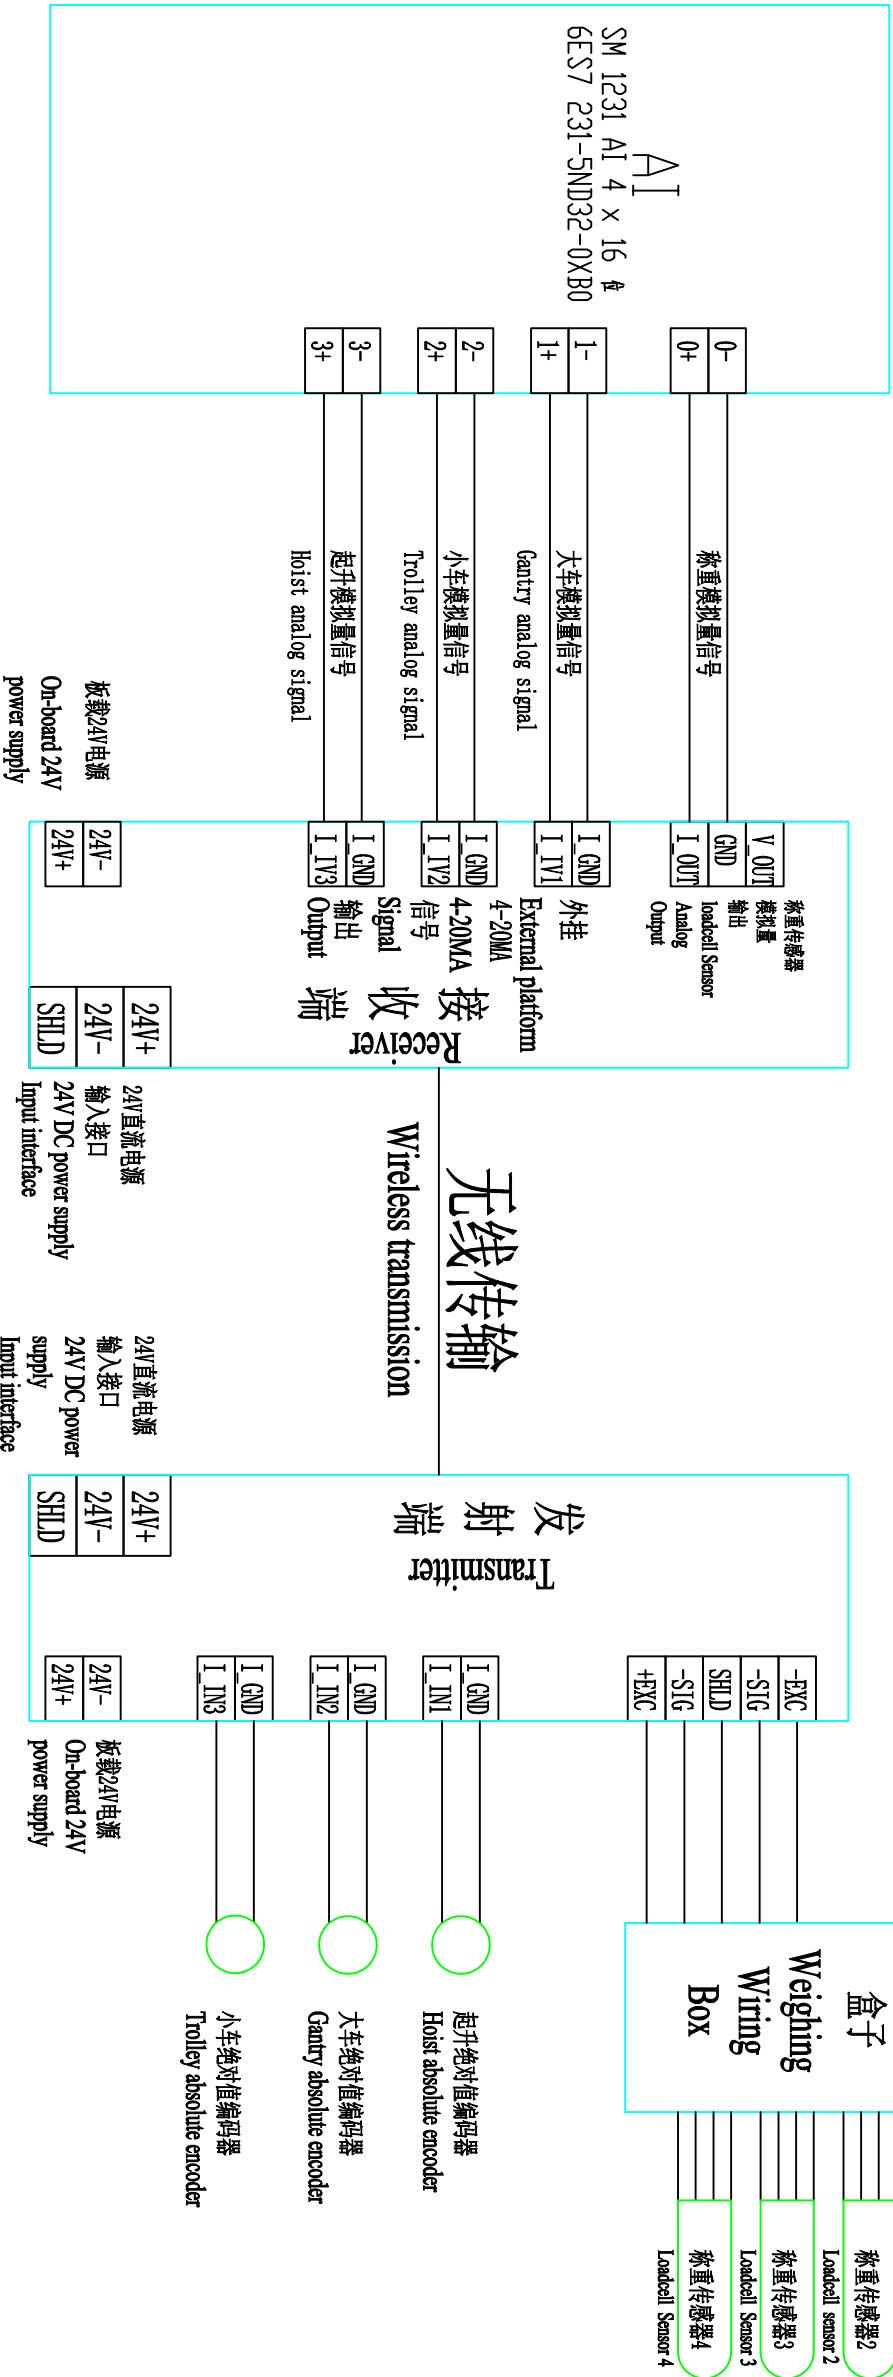

d						Designed by	
C						Reviewed by	
b						Chief Designer	
a							
Sheet No.		Change No.	Signature	Date			
Item		Description	名称	项 目			
Municipal solid waste incineration power plant		城市生活垃圾焚烧发电厂	项 目				
Bridge Crane of Ash Handling Grab		灰渣桥式抓斗起重机	项 目				
Add: Lingyuzan Industrial Zone, Jindong District, Jinhu City, Zhejiang Province		地址: 浙江省金华市金东区岭下朱工业区	项 目				
Zhejiang Zheqi Machinery Co., Ltd.		浙江浙起机械有限公司	项 目				
Encoder and Loadcell Diagram		称重和编码器 图纸	项 目				
DWG No.		图 号	项 目				
= 01		图 号	项 目				
1		图 号	项 目				
ZQ02/0103-A		图 号	项 目				
This page		图 号	项 目				
1		图 号	项 目				