


输出速度组合
Output speed combination

DI 1 号 Terminals	2 号 Speed 2	3 号 Speed 3
DI3	1	0
DI4	1	1

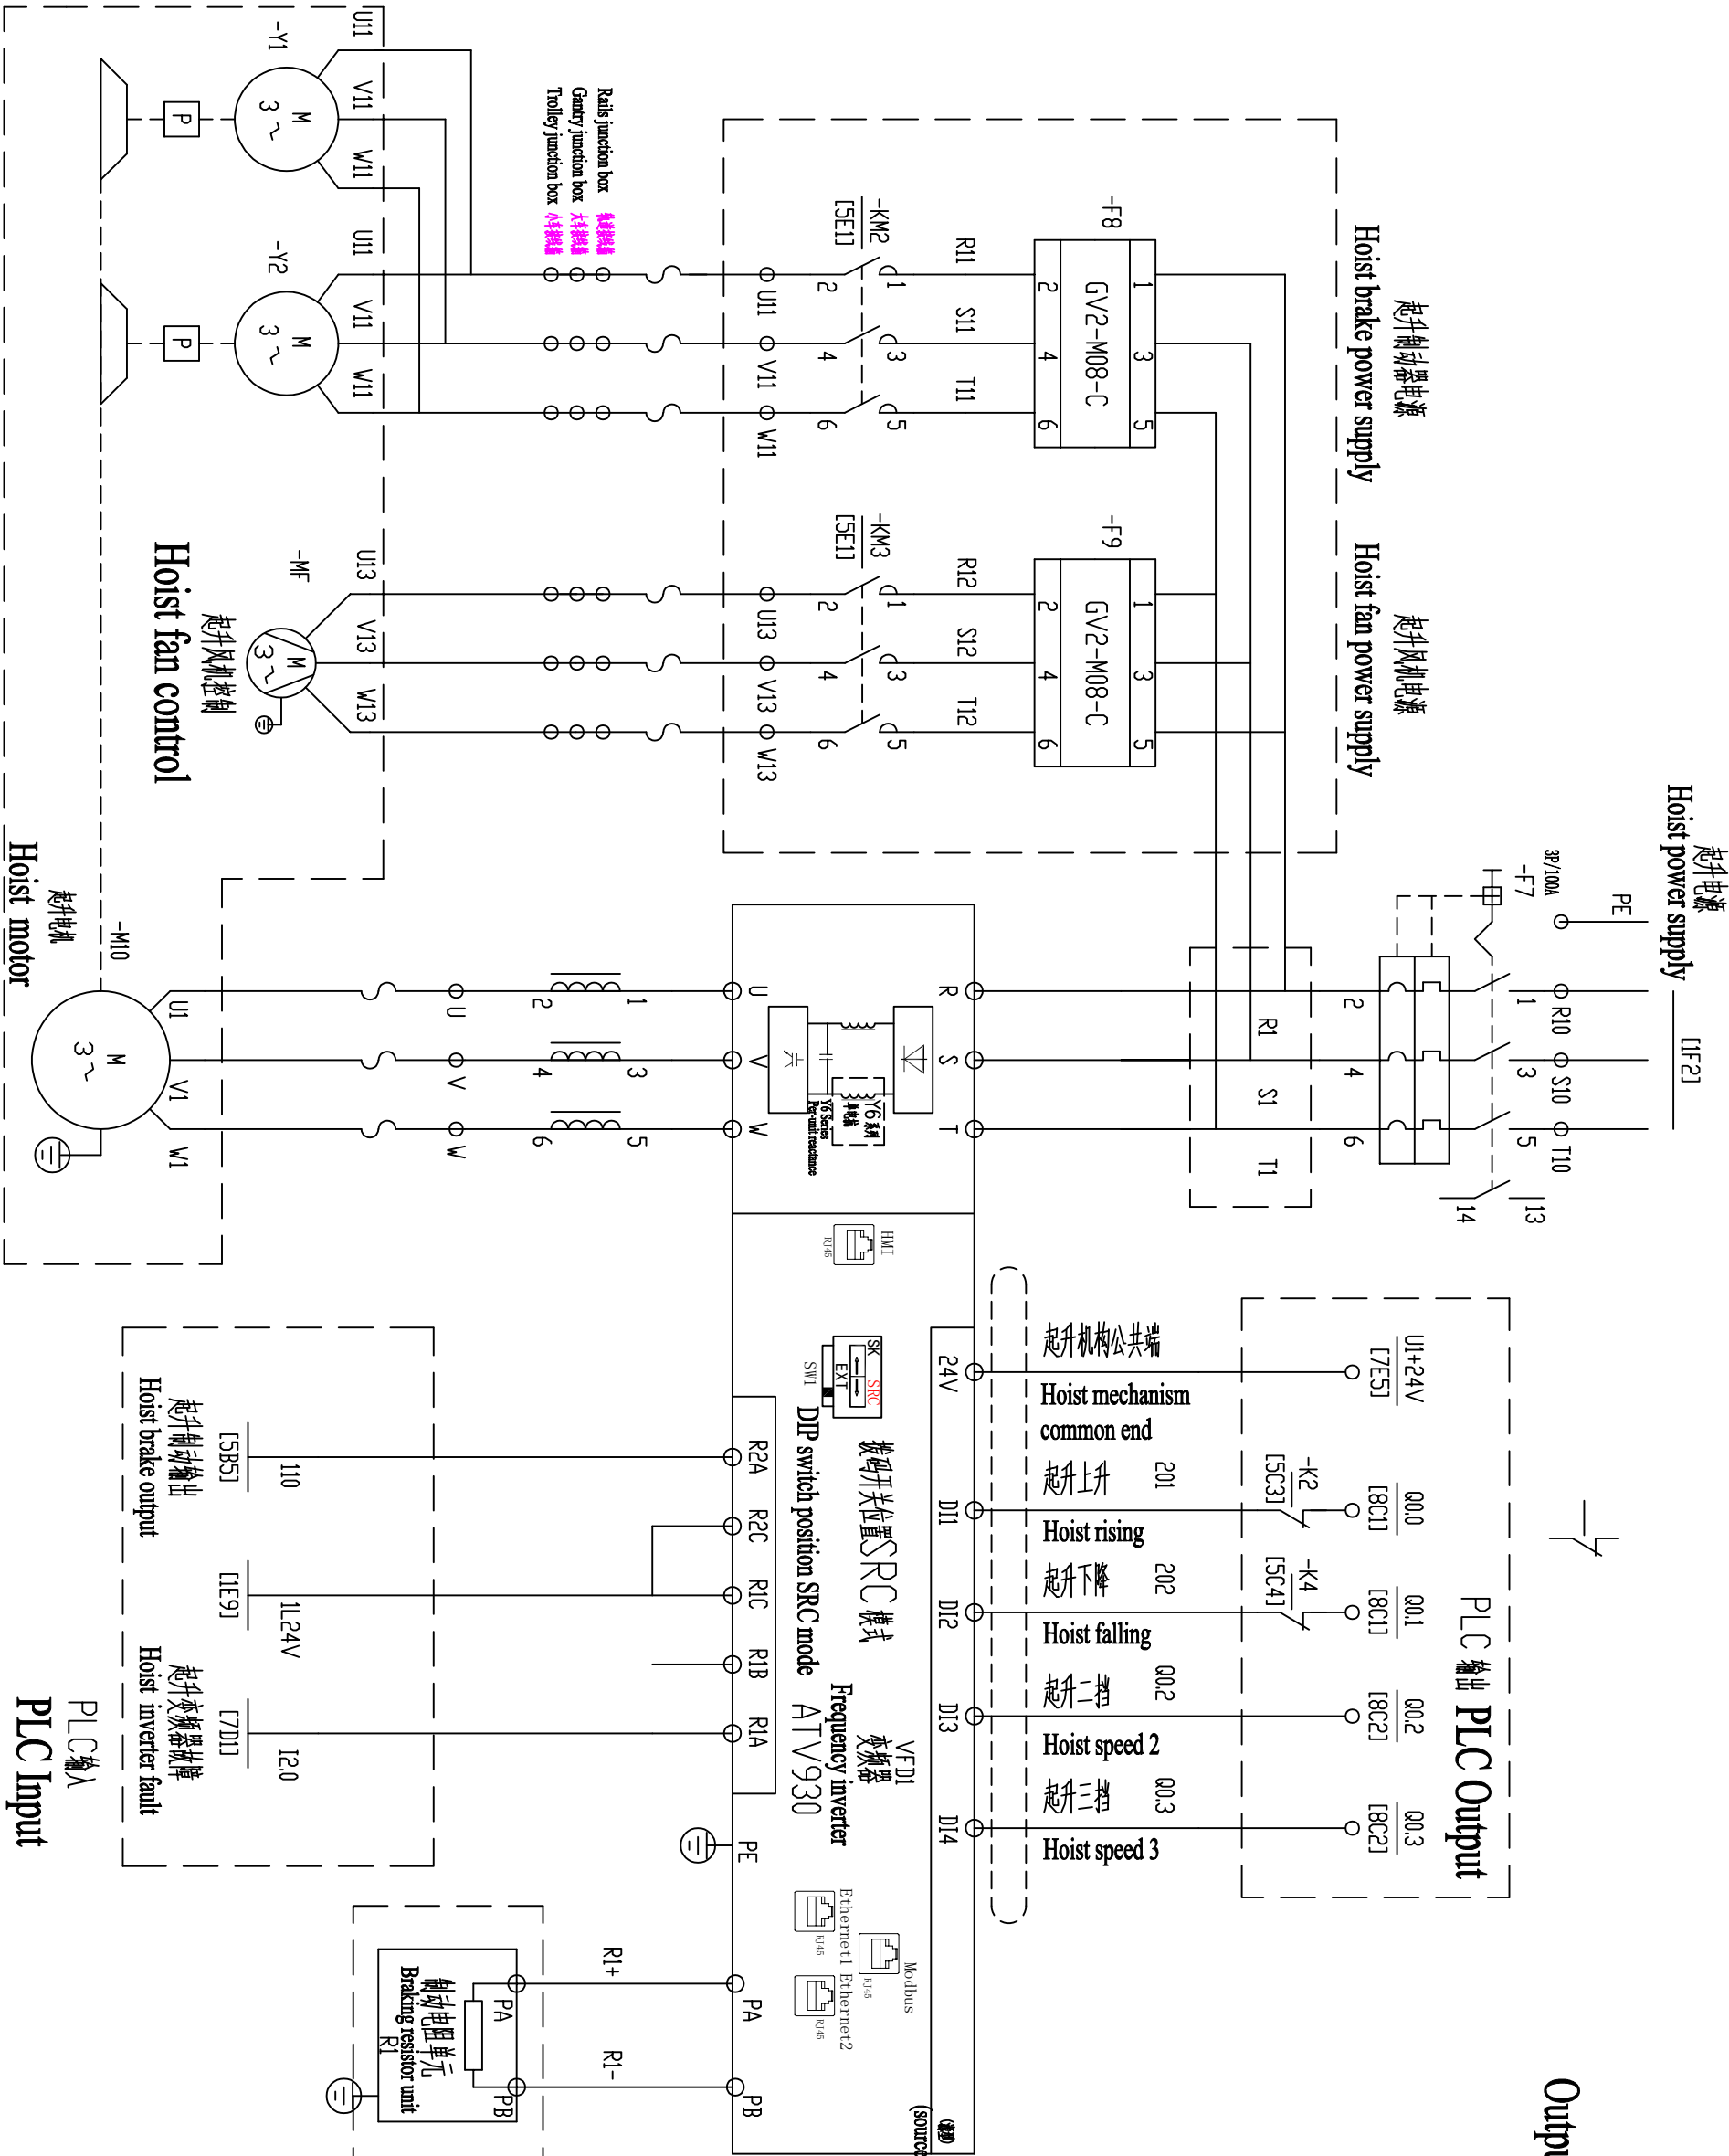

项 目		Designed by		Reviewed by	
Item		Municipal solid waste incineration power plant		Chief Designer	
Description		Electrical Schematic Diagram of Ash Handling Crane		Chief Designer	
名称		起升机构		图 号	
Description		Hoist mechanism		DWG No.	
数量		Scale		= 01	
质量		Sheet		9	
数量		of		2	