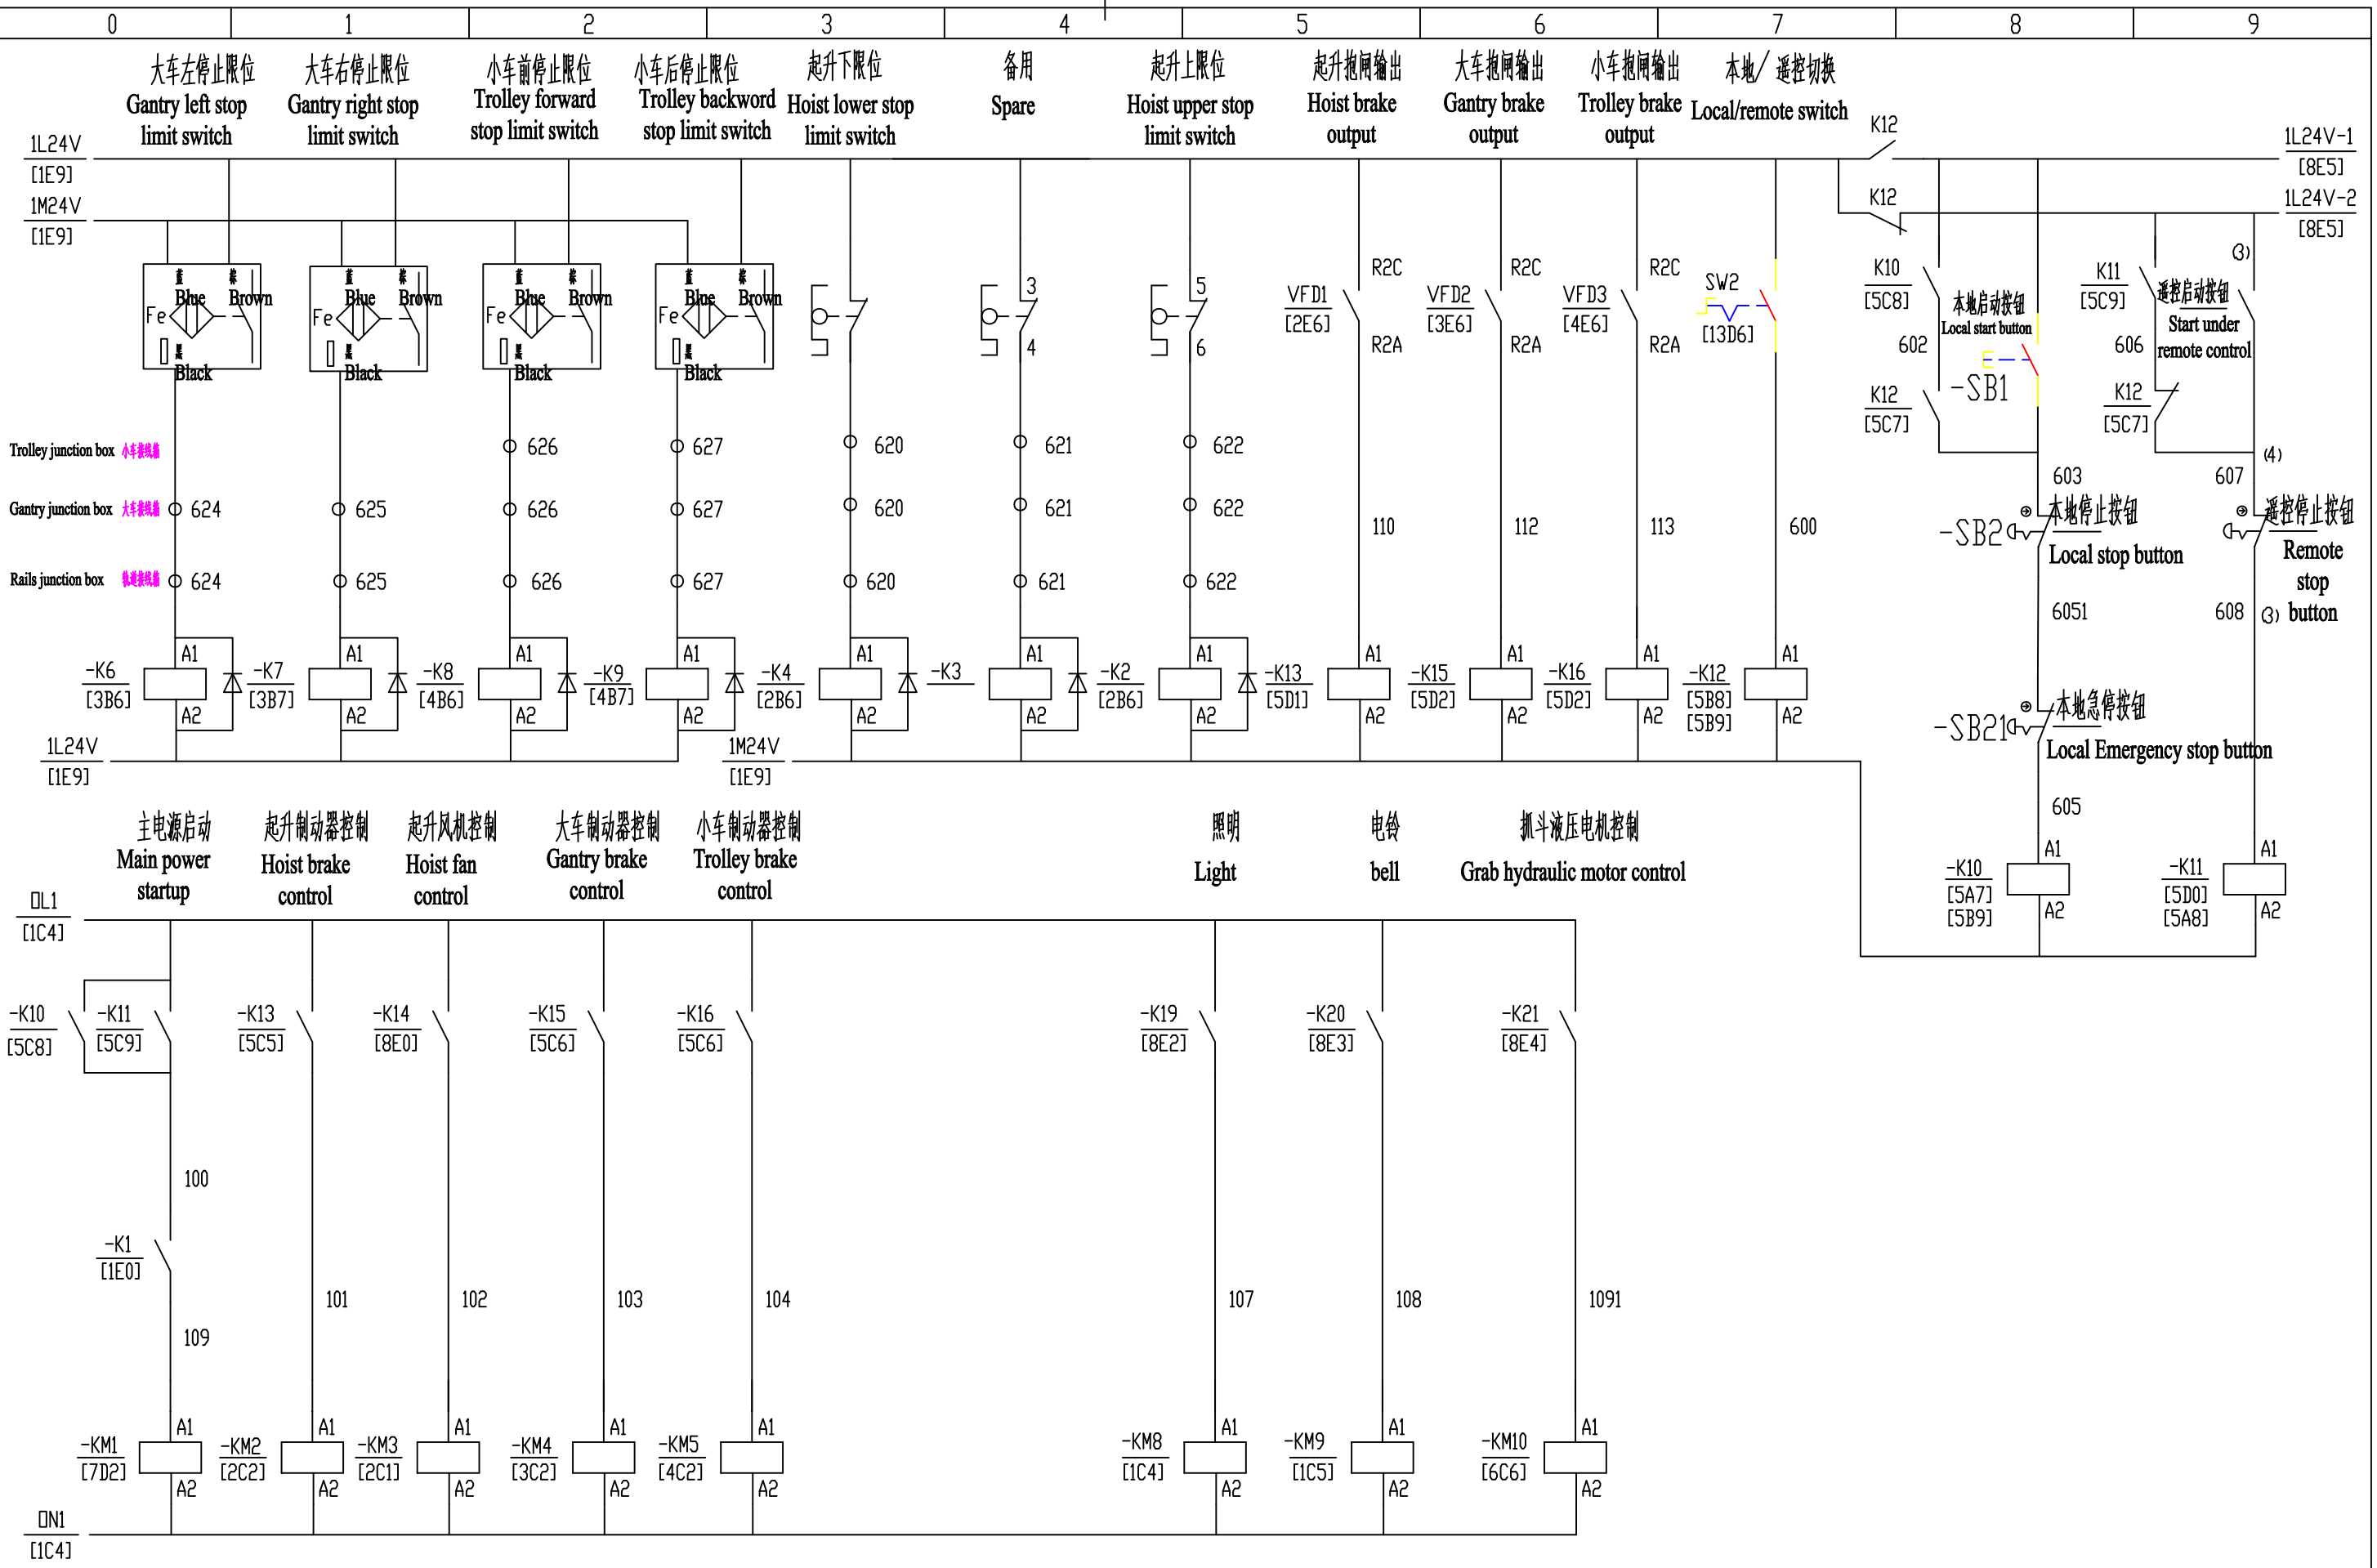

图纸总数 Total sheet	**
借(领)用登记 Borrowed (General) Parts Registration	
描 图 Traced by	
校 对 Checked by	
旧底图总号 General No. of Old Traced Drawing	
底图总号 Base Drawing Total No.	
签 字 Signature	
日 期 Date	

标记 Mark	处数 Nos.	更改单号 Changed File No.	签字 Signature	日期 Date	
d					设 计 Designed by
c					审 查 Reviewed by
b					主管设计 Chief Designer
a					

项 目 Item	城市生活垃圾焚烧发电厂 灰渣抓斗桥式起重机 Municipal solid waste incineration power plant Bridge Crane of Ash Handling Grab
名 称 Description	灰渣吊电气原理图 Electrical Schematic Diagram of Ash Handling Crane

浙江浙起机械有限公司 Zhejiang Zheqi Machinery Co., Ltd.
地址：浙江省金华市金东区岭下朱工业区 Add: Lingxiazhu Industrial Zone, Jindong District, Jinhua City, Zhejiang Province

名 称 Description	继电器控制 Relay control	图 号 DWG No.	ZQQZ/0103-5
质 量 Quality		比 例 Scale	= 01 / + **
		张 次 Sheet	9
下页 Next page	6	本页 This page	5
共 张 of	5		