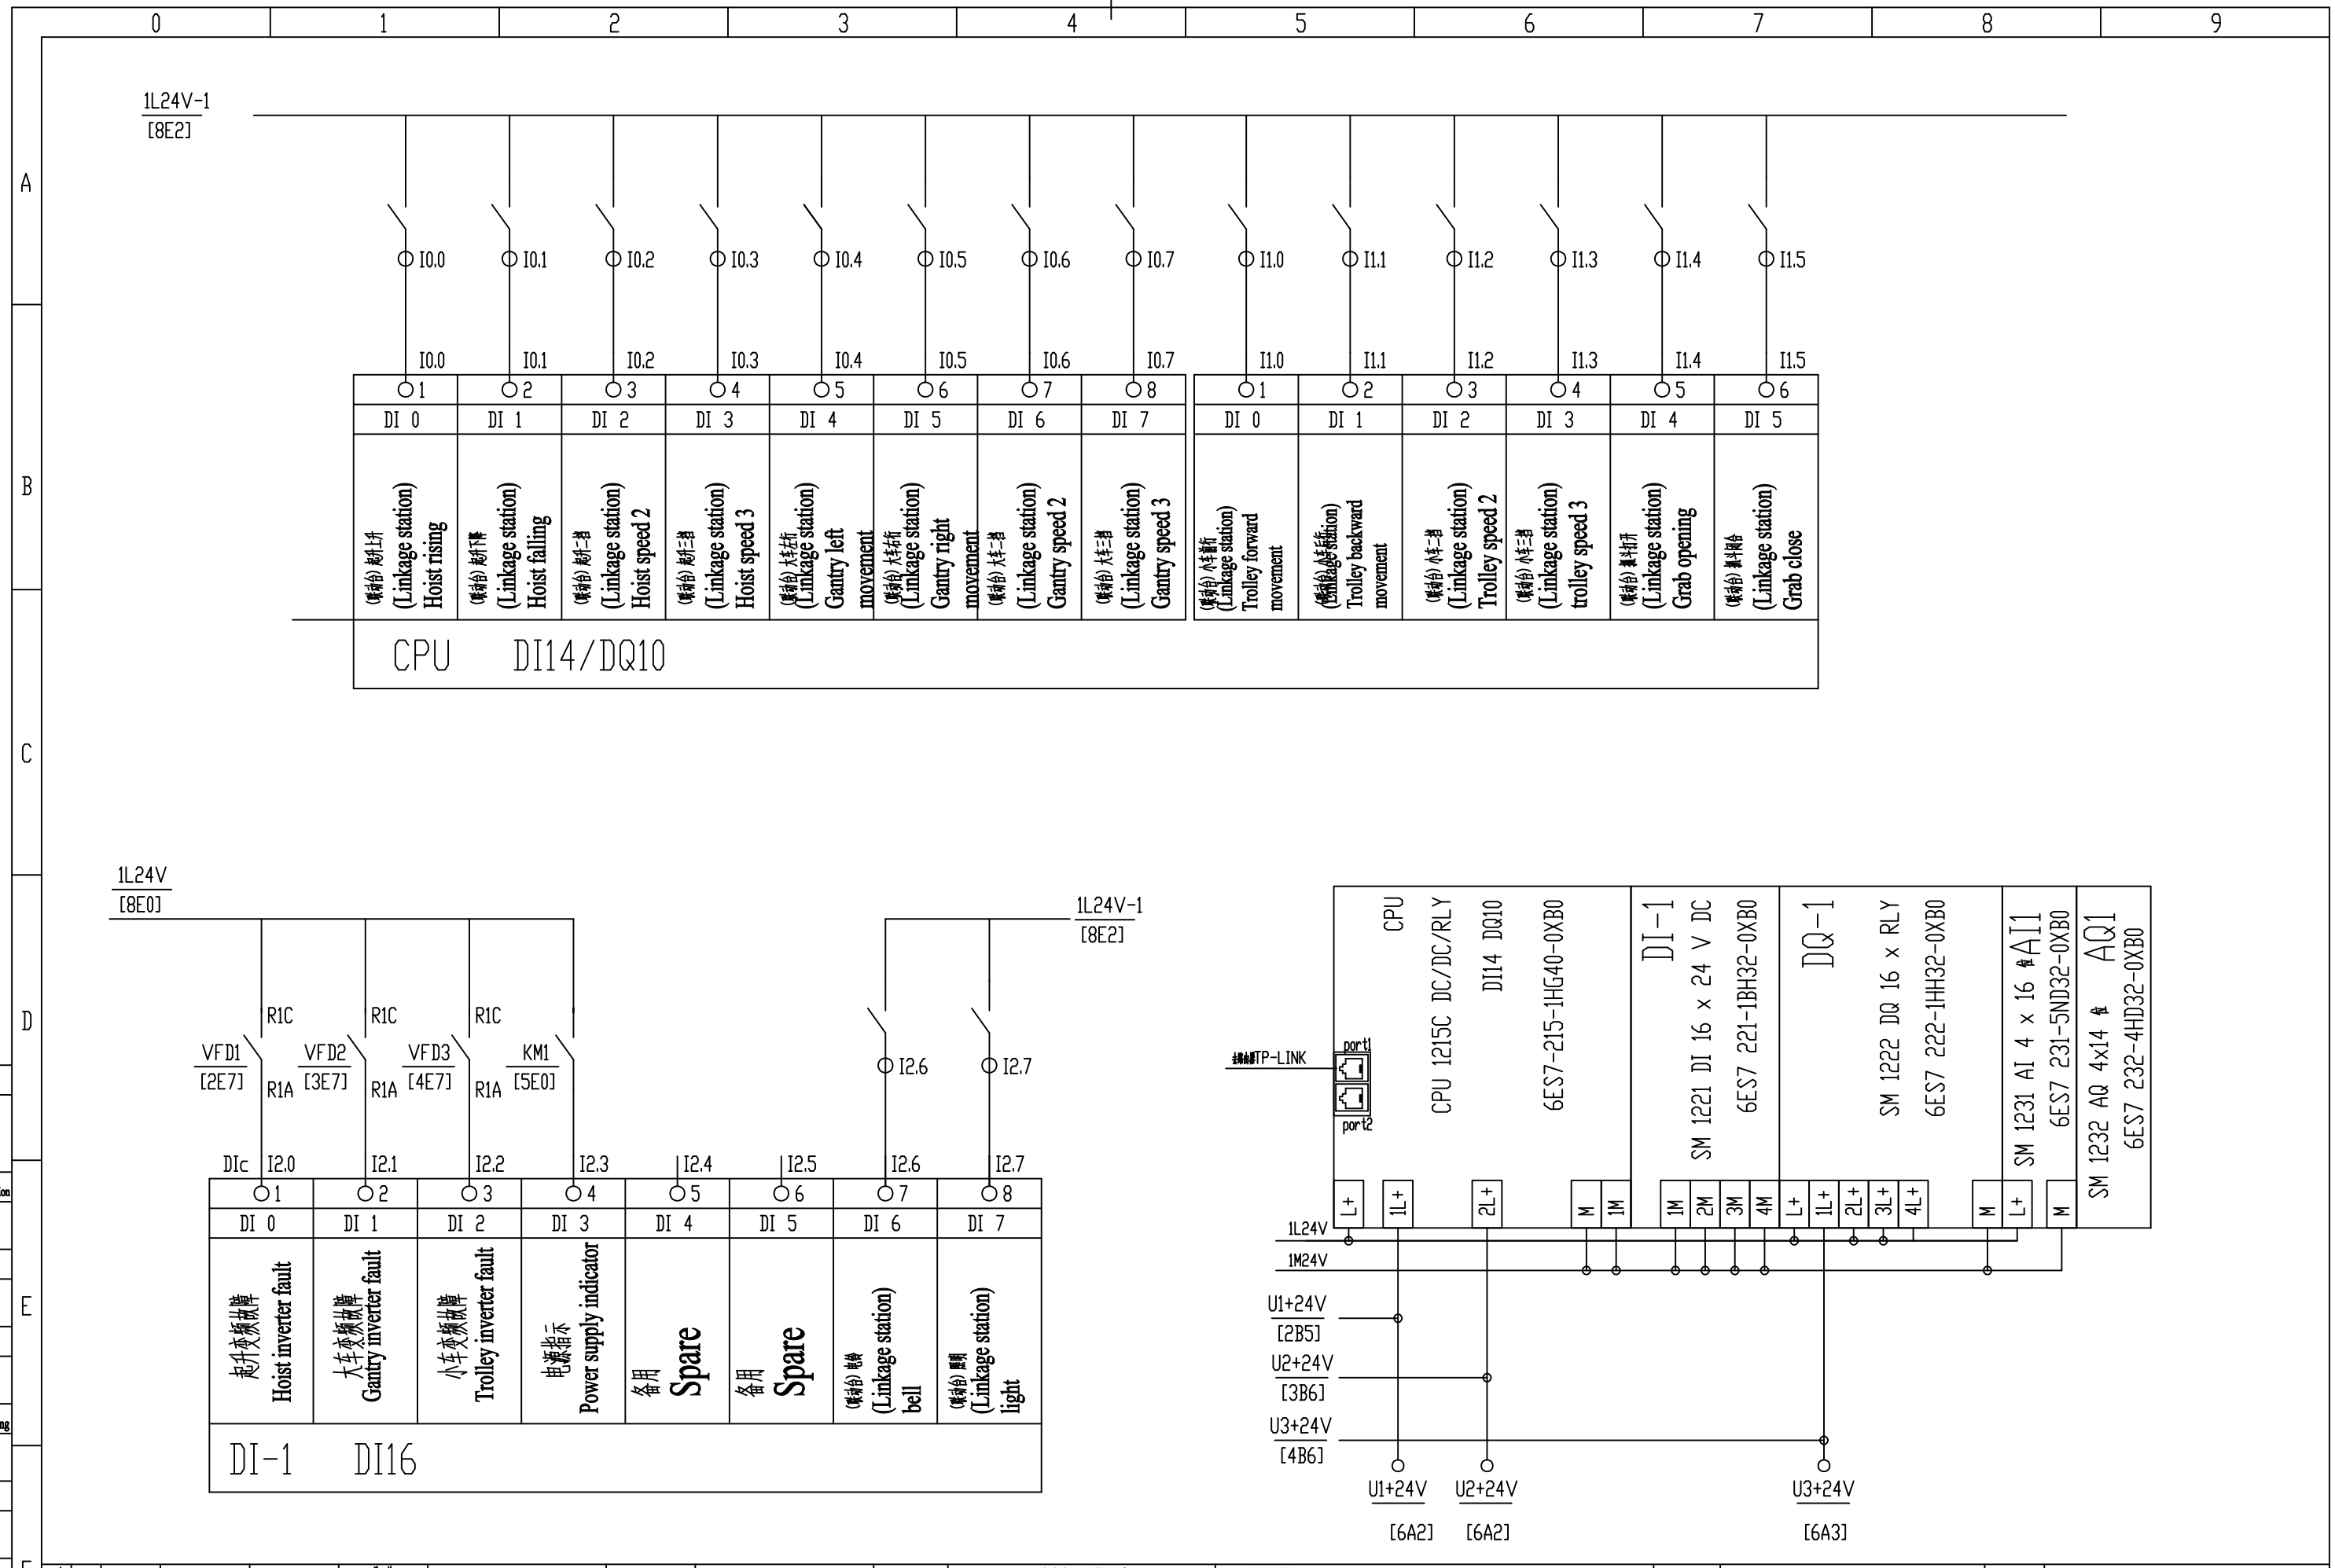

d					设计 Designed by			
c					审查 Reviewed by			
b					主管设计 Chief Designer			
a								
标记 Mark	处数 Nos.	更改文件号 Changed File No.	签字 Signature	日期 Date				

项目 Item	城市生活垃圾焚烧发电厂 灰渣抓斗桥式起重机 Municipal solid waste incineration power plant Bridge Crane of Ash Handling Grab	浙江浙起机械有限公司 Zhejiang Zheqi Machinery Co., Ltd. 地址：浙江省金华市金东区岭下朱工业区 Add: Lingxiazhu Industrial Zone, Jindong District, Jinhua City, Zhejiang Province	名称 Description	PLC/输入 PLC/input	图号 DWG No. ZQQZ/0103-7
名称 Description	灰渣吊电气原理图 Electrical Schematic Diagram of Ash Handling Crane		质量 Quality	比例 Scale	下页 Next page 8 本页 This page 7
					= 01 + **
					张数 Sheet 9 张次 of 7

Total sheet
**
Borrowed (General) Parts Registration
Traced by
Checked by
General No. of Old Traced Drawing
Base Drawing Total No.
Signature
Date