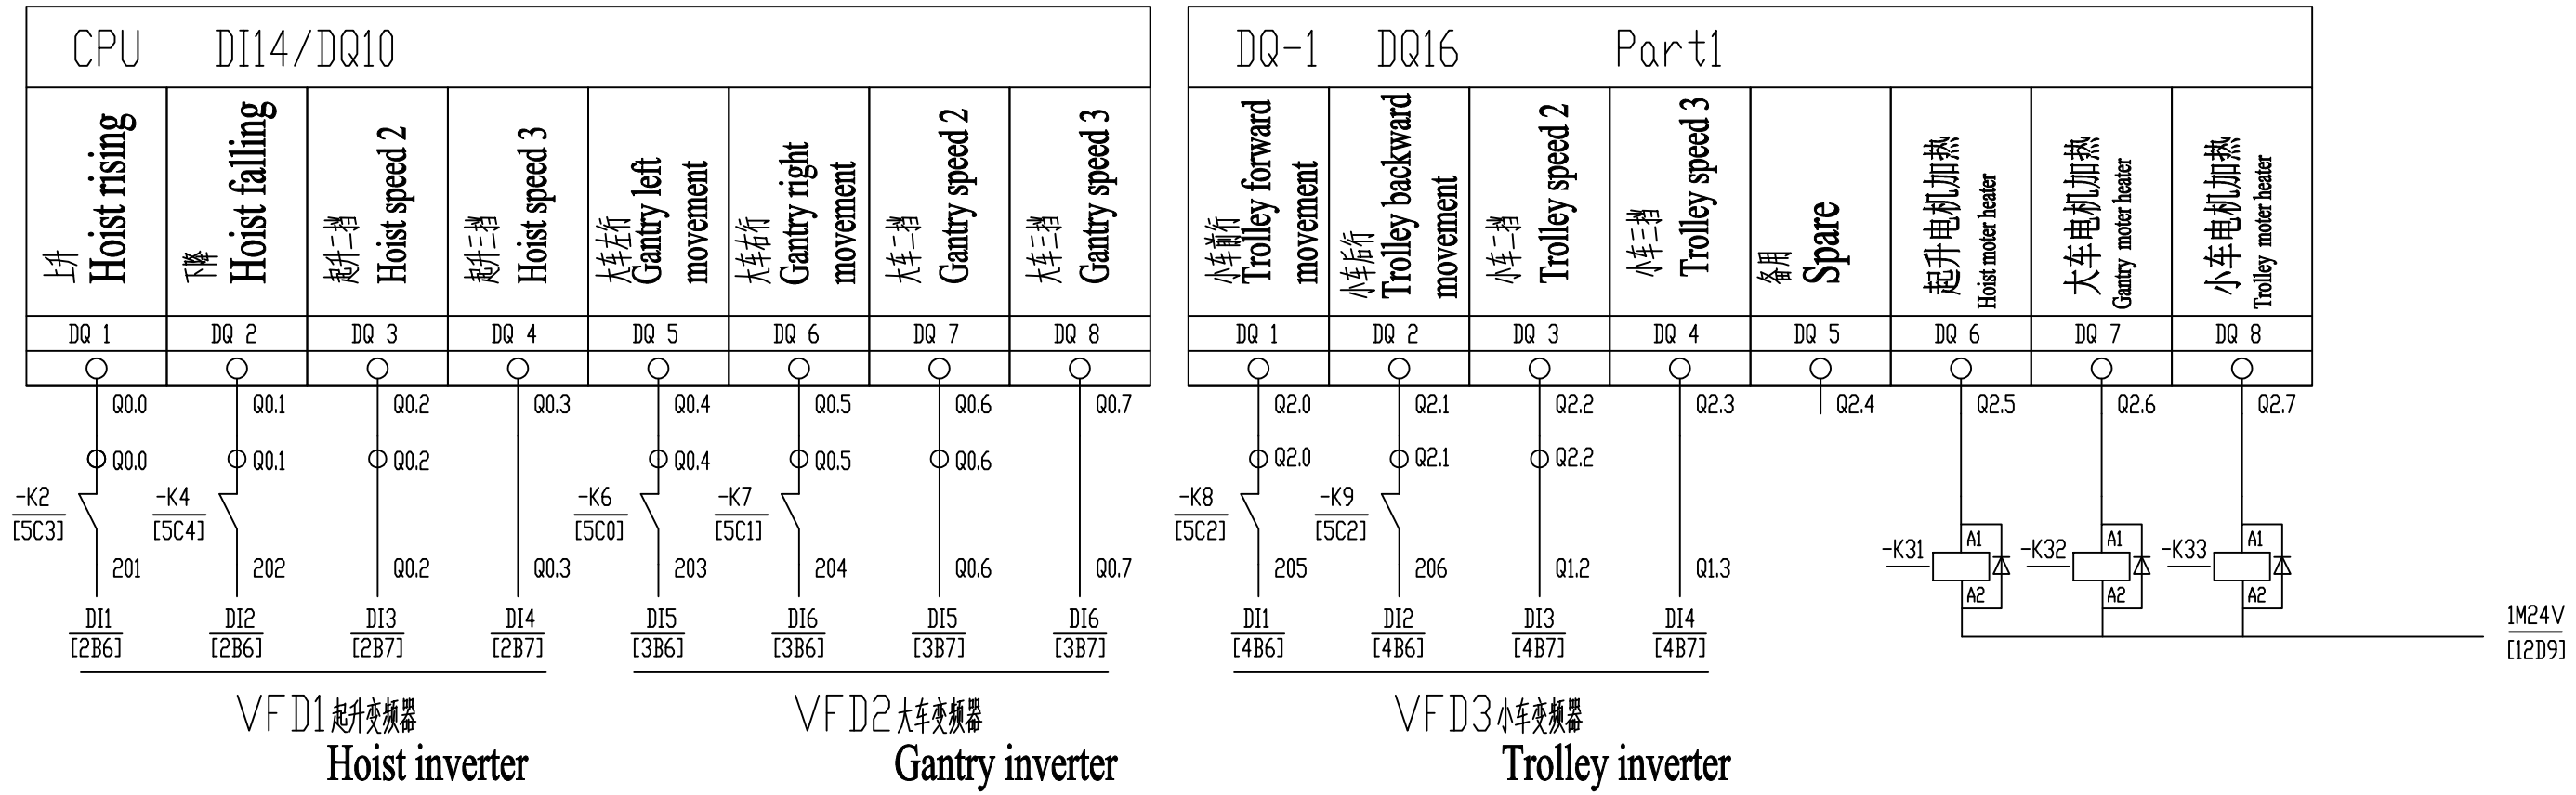

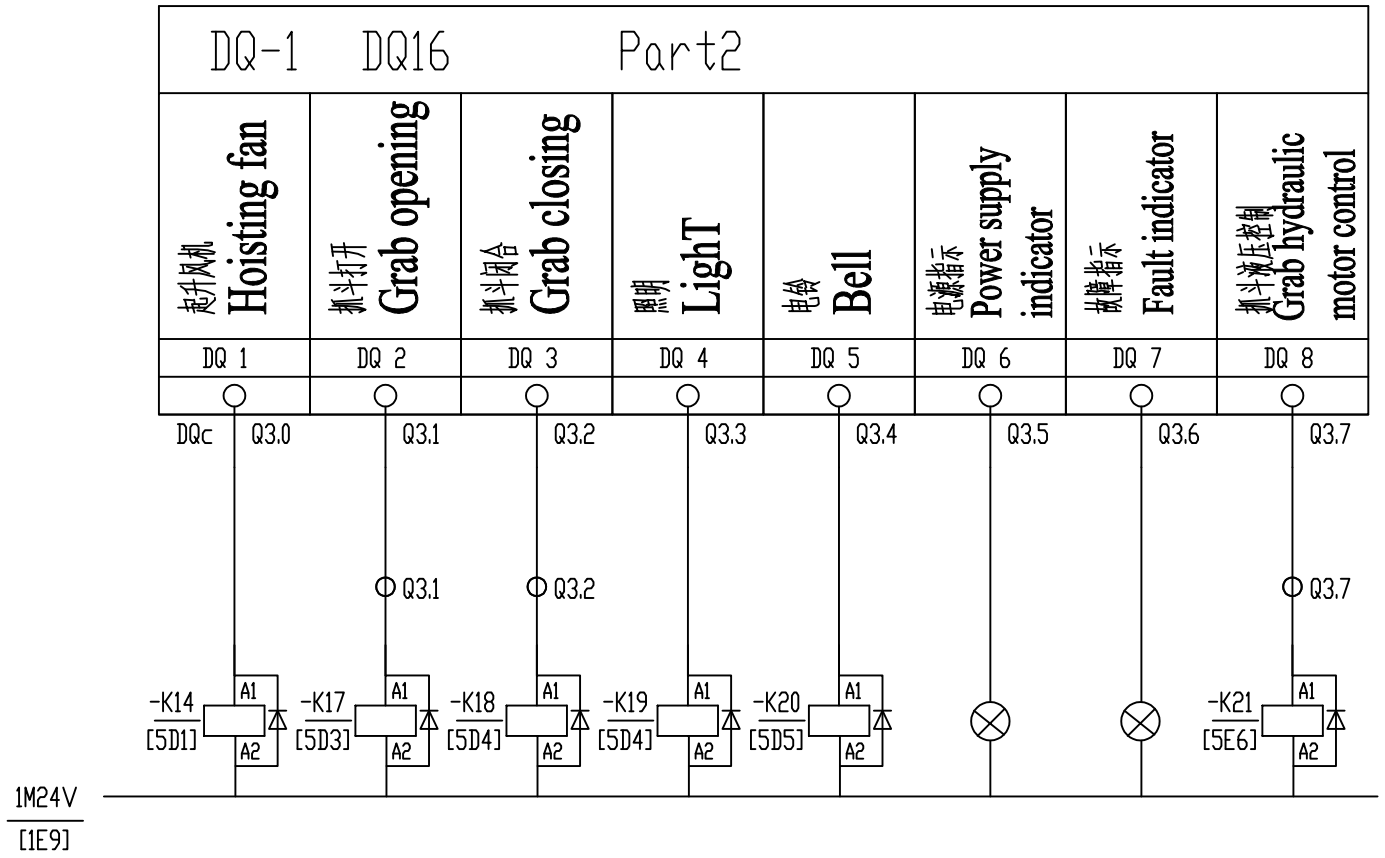

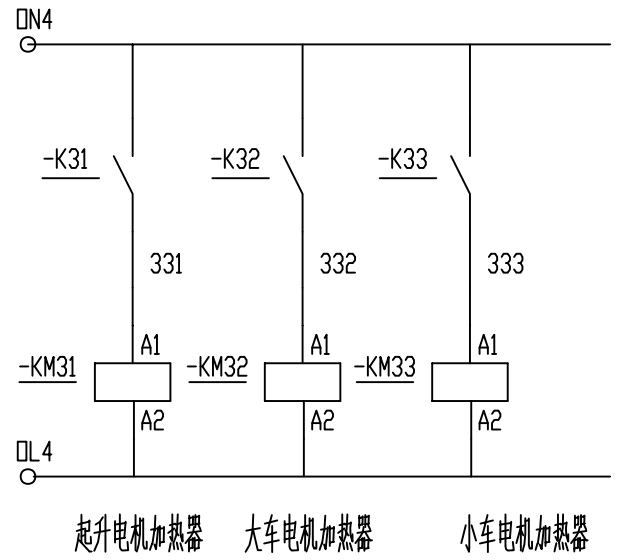

d					设计 Designed by			
c					审查 Reviewed by			
b					主管设计 Chief Designer			
a								
标记 Mark	处数 Nos.	更改文件号 Changed File No.	签字 Signature	日期 Date				

项目 Item	城市生活垃圾焚烧发电厂 抓斗桥式起重机 Municipal solid waste incineration power plant Bridge Crane of Ash Handling Grab
名称 Description	抓斗吊电气原理图 Electrical Schematic Diagram of Ash Handling Crane

浙江浙起机械有限公司
Zhejiang Zheqi Machinery Co., Ltd.
地址：浙江省金华市金东区岭下朱工业区
Add: Lingxiazhu Industrial Zone, Jindong District, Jinhua City, Zhejiang Province

名称 Description	PLC/输出 PLC/output	图号 DWG No.	ZQQZ/0103-8
质量 Quality		比例 Scale	= 01
			+ **
		张次 Sheet	9
		共 of	8

下页 Next page 9 本页 This page 8

Total sheet **

Borrowed (General) Parts Registration

Traced by

Checked by

General No. of Old Traced Drawing

Base Drawing Total No.

Signature

Date