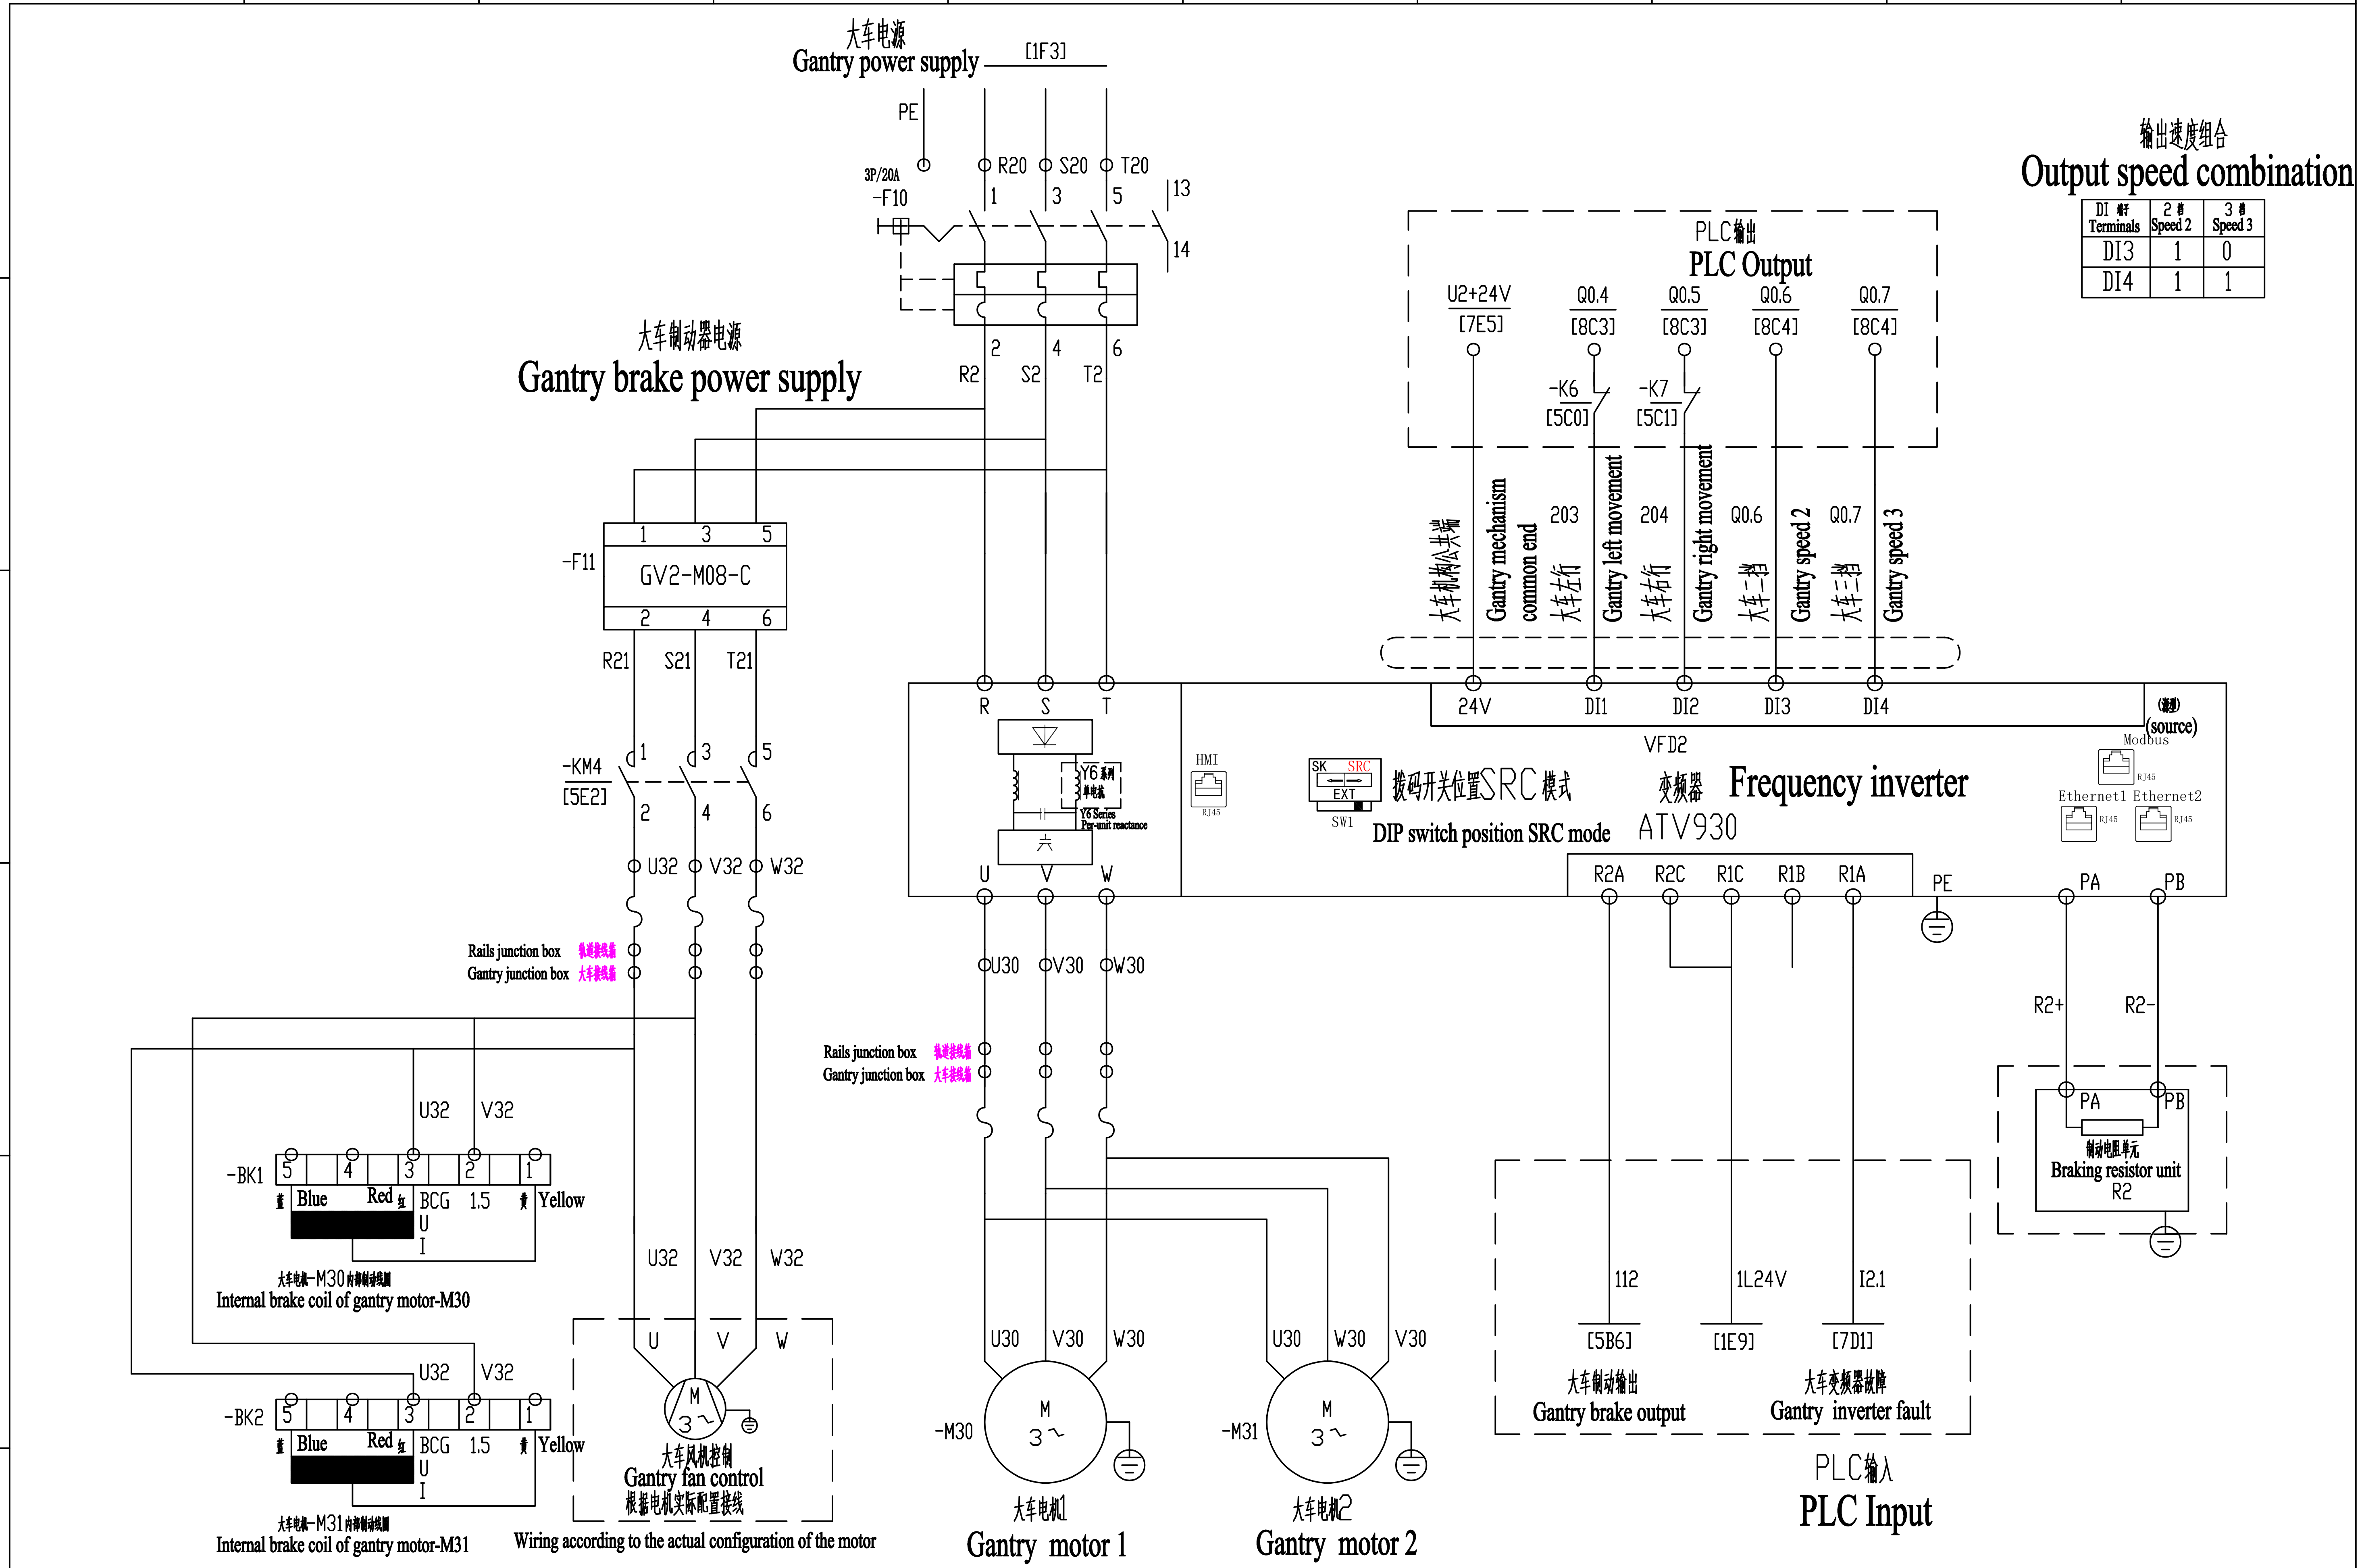

## 输出速度组合
## Output speed combination

| DI 端子<br>Terminals | 2 档<br>Speed 2 | 3 档<br>Speed 3 |
|---|---|---|
| DI3 | 1 | 0 |
| DI4 | 1 | 1 |

图纸总张次
Total sheet

✳✳

借(通)用件登记
Borrowed (General) Parts Registration

描图
Traced by

描校
Checked by

旧底图总号
General No. of Old Traced Drawing

底图总号
Base Drawing Total No.

签字
Signature

日期
Date

| 标记<br>Mark | 处数<br>Nos. | 更改文件号<br>Changed File No. | 签字<br>Signature | 日期<br>Date | | |
|---|---|---|---|---|---|---|
| d | | | | | 设计<br>Designed by | |
| c | | | | | 审查<br>Reviewed by | |
| b | | | | | 主管设计<br>Chief Designer | |
| a | | | | | | |

项目
Item

城市生活垃圾焚烧发电厂
灰渣抓斗桥式起重机
Municipal solid waste incineration power plant
Bridge Crane of Ash Handling Grab

名称
Description

灰渣吊电气原理图
Electrical Schematic Diagram of Ash Handling Crane

浙江浙起机械有限公司
Zhejiang Zheqi Machinery Co., Ltd.
地址：浙江省金华市金东区岭下朱工业区
Add: Lingxiazhu Industrial Zone, Jindong District, Jinhua City, Zhejiang Province

名称
Description

大车机构
Gantry mechanism

质量
Quality

比例
Scale

图号
DWG No.

ZQQZ/0103-3

下页
Next page 4

本页
This page 3

= 01

+ ✳✳

张数
Sheet 9

张次
of 3