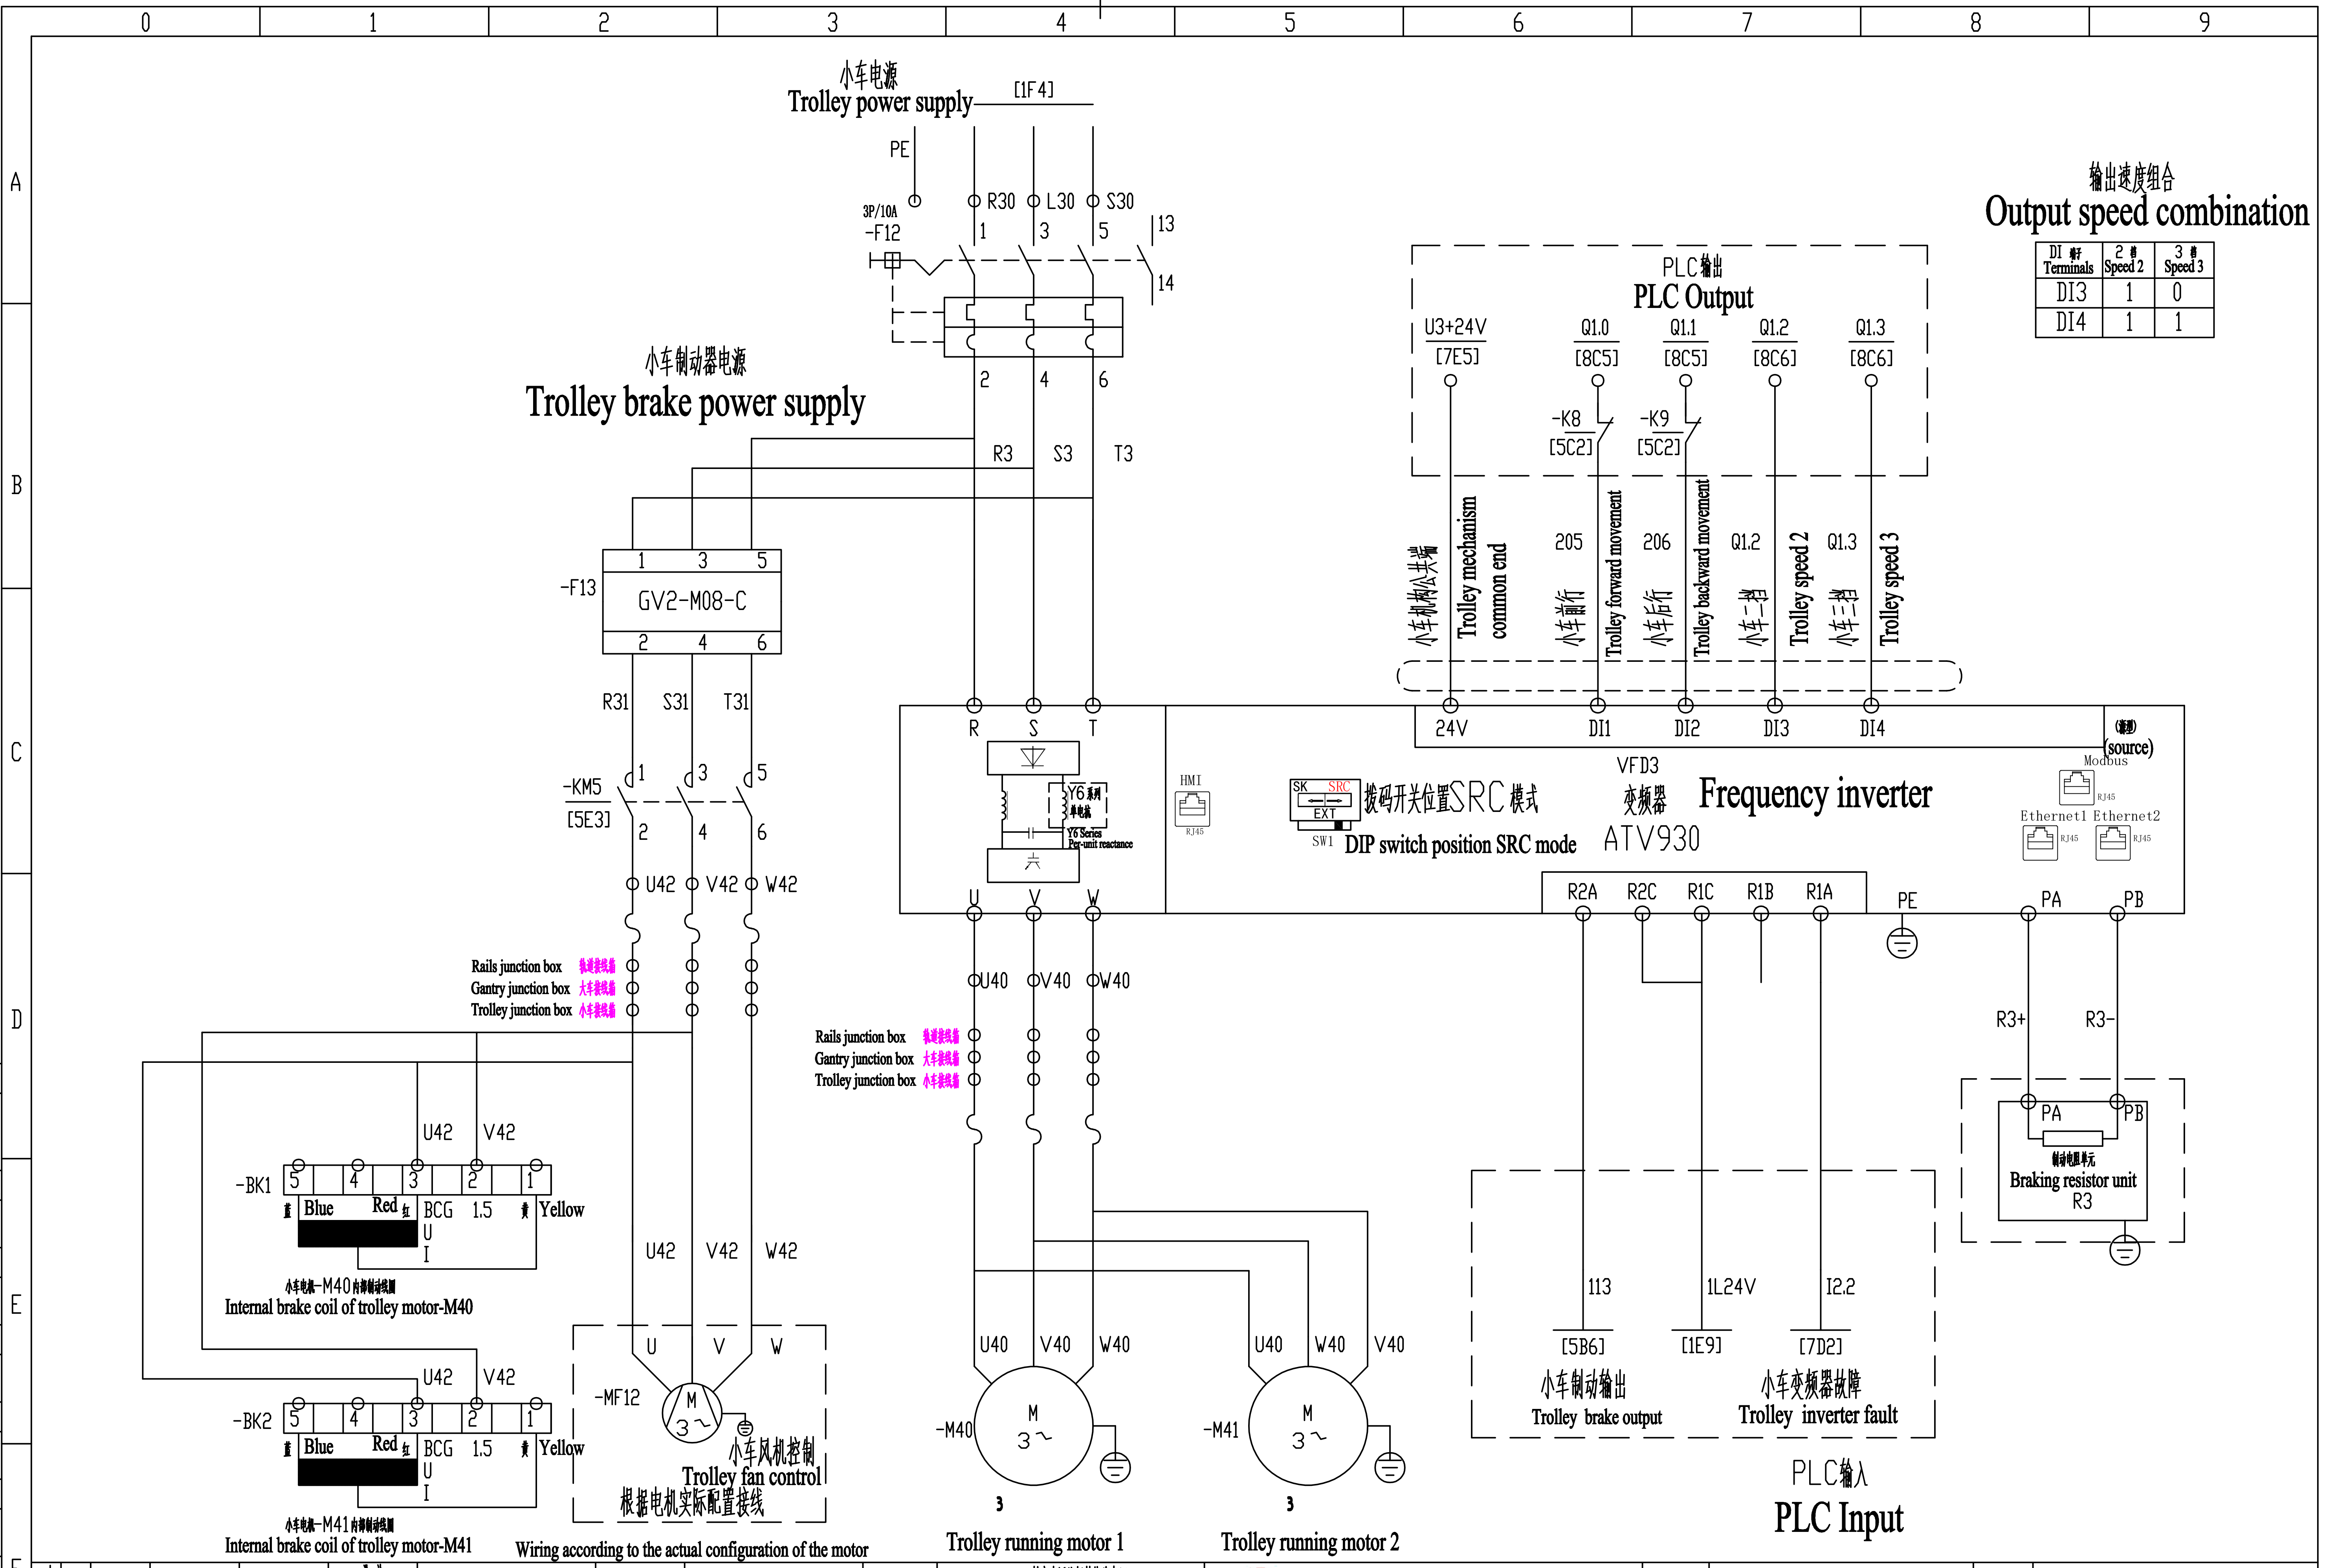

输出速度组合
Output speed combination

DI 端子 Terminals	2 档 Speed 2	3 档 Speed 3
DI3	1	0
DI4	1	1

项 目 Item	城市生活垃圾焚烧发电厂 灰渣抓斗桥式起重机 Municipal solid waste incineration power plant Bridge Crane of Ash Handling Grab	浙江浙起机械有限公司 Zhejiang Zheqi Machinery Co., Ltd. 地址：浙江省金华市金东区岭下朱工业区 Add: Lingxiazhu Industrial Zone, Jindong District, Jinhua City, Zhejiang Province	名 称 Description: 小车机构 Trolley mechanism
名 称 Description	灰渣吊电气原理图 Electrical Schematic Diagram of Ash Handling Crane		质 量 Quality 比 例 Scale

图 号
DWG No. ZQQZ/0103-4

下页
Next page 5

本页
This page 4

= 01

+ ※※

共 张
Sheet 9

第 张
of 4

标记 Mark	处数 Nos.	更改文件号 Changed File No.	签 字 Signature	日 期 Date
d				
c				
b				
a				

设 计
Designed by

审 核
Reviewed by

主管设计
Chief Designer

图纸总张数
Total sheet

※※

借（通）用件登记
Borrowed (General) Parts Registration

描 图
Traced by

校 对
Checked by

旧底图总号
General No. of Old Traced Drawing

底图总号
Base Drawing Total No.

签 字
Signature

日 期
Date