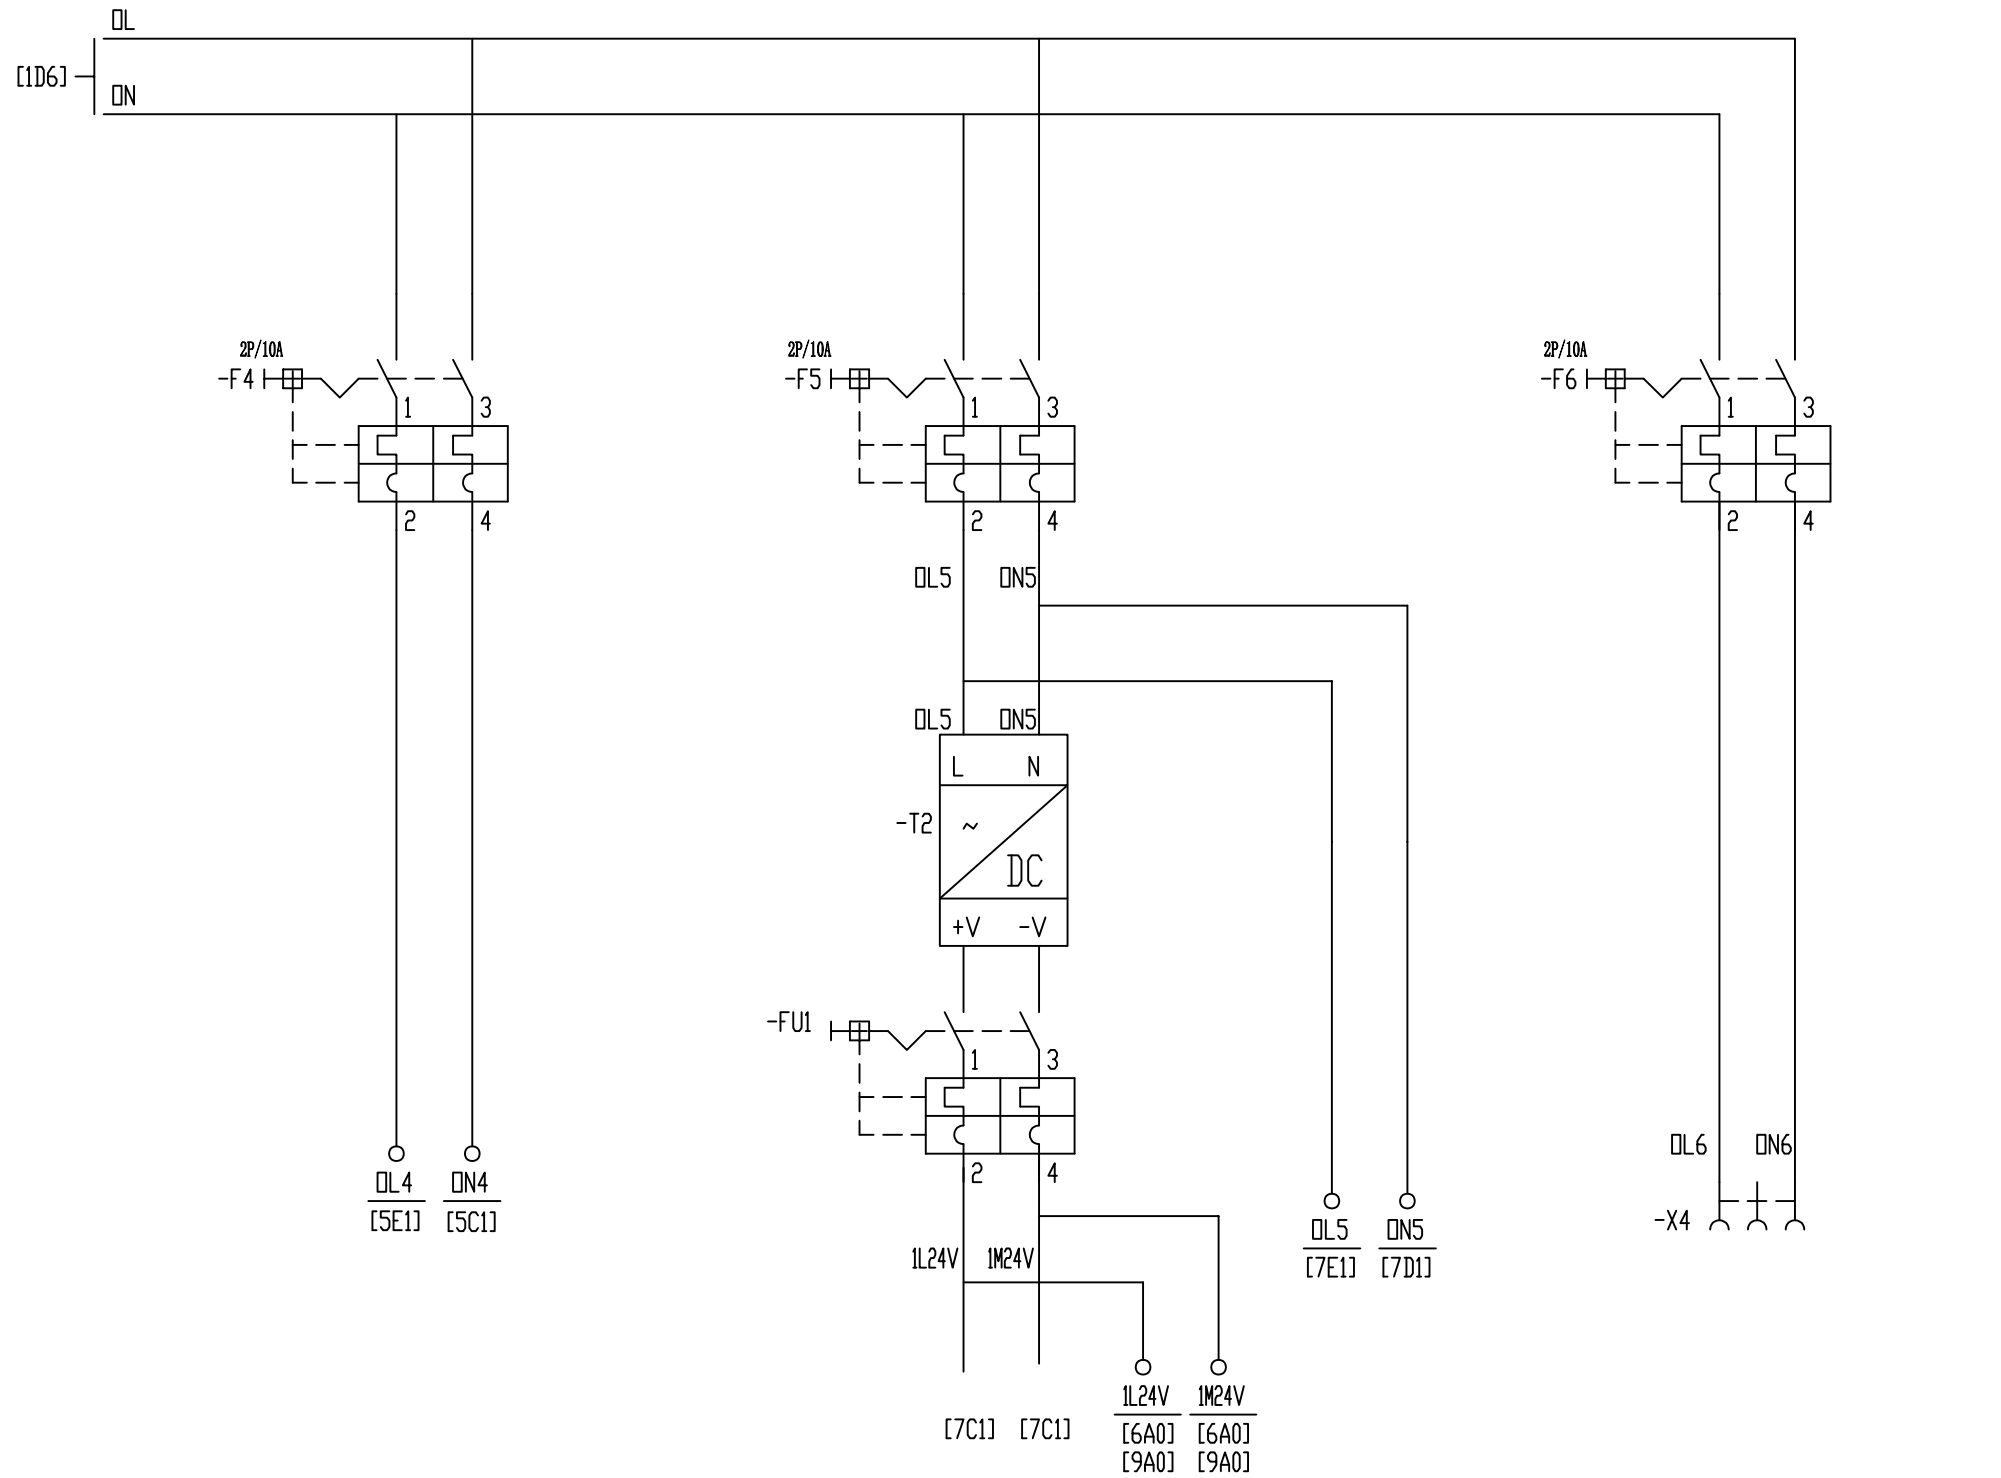


d					设 计 Designed by	孙佳炜 Sun Jiawei			项 目 Item	城市生活垃圾焚烧发电厂 垃圾抓斗桥式起重机 Municipal solid waste incineration power plant Waste grab bridge crane
c					审 查 Reviewed by	董辰 Dong Chen				
b					主管设计 Chief Designer	石振 Shi Zhen				18t 37.1m A8
a										
标记 Mark	处数 Nos.	更改文件号 Changed File No.	签字 Signature							

浙江浙起机械有限公司
Zhejiang Zheqi Machinery Co., Ltd.
地址：浙江省金华市金东区岭下朱工业区
Add: Lingxiazhu Industrial Zone, Jindong District, Jinhua City, Zhejiang Province

名 称 Description	配电保护 Distribution protection			图 号 DWG No.	QZL/0101-8
质 量 Quality		比 例 Scale		下张 Next page	9
				本张 This page	8
				张 数 Sheet	14
				张 次 Sheet Of	8

图纸总张次 Total sheet	**
借(通)用件登记 Borrowed (General) Parts Registration	
描 Traced by 图	
描 Checked by 校	
旧底图总号 General No. of Old Traced Drawing	
底图总号 Base Drawing Total No.	
签 Signature 字	
日 Date 期	