
Linkage Panel
Analog input module
联动台
模拟量输入模块

无线称重仪表ZQ161RF
Wireless loadcell instrument ZQ161RF

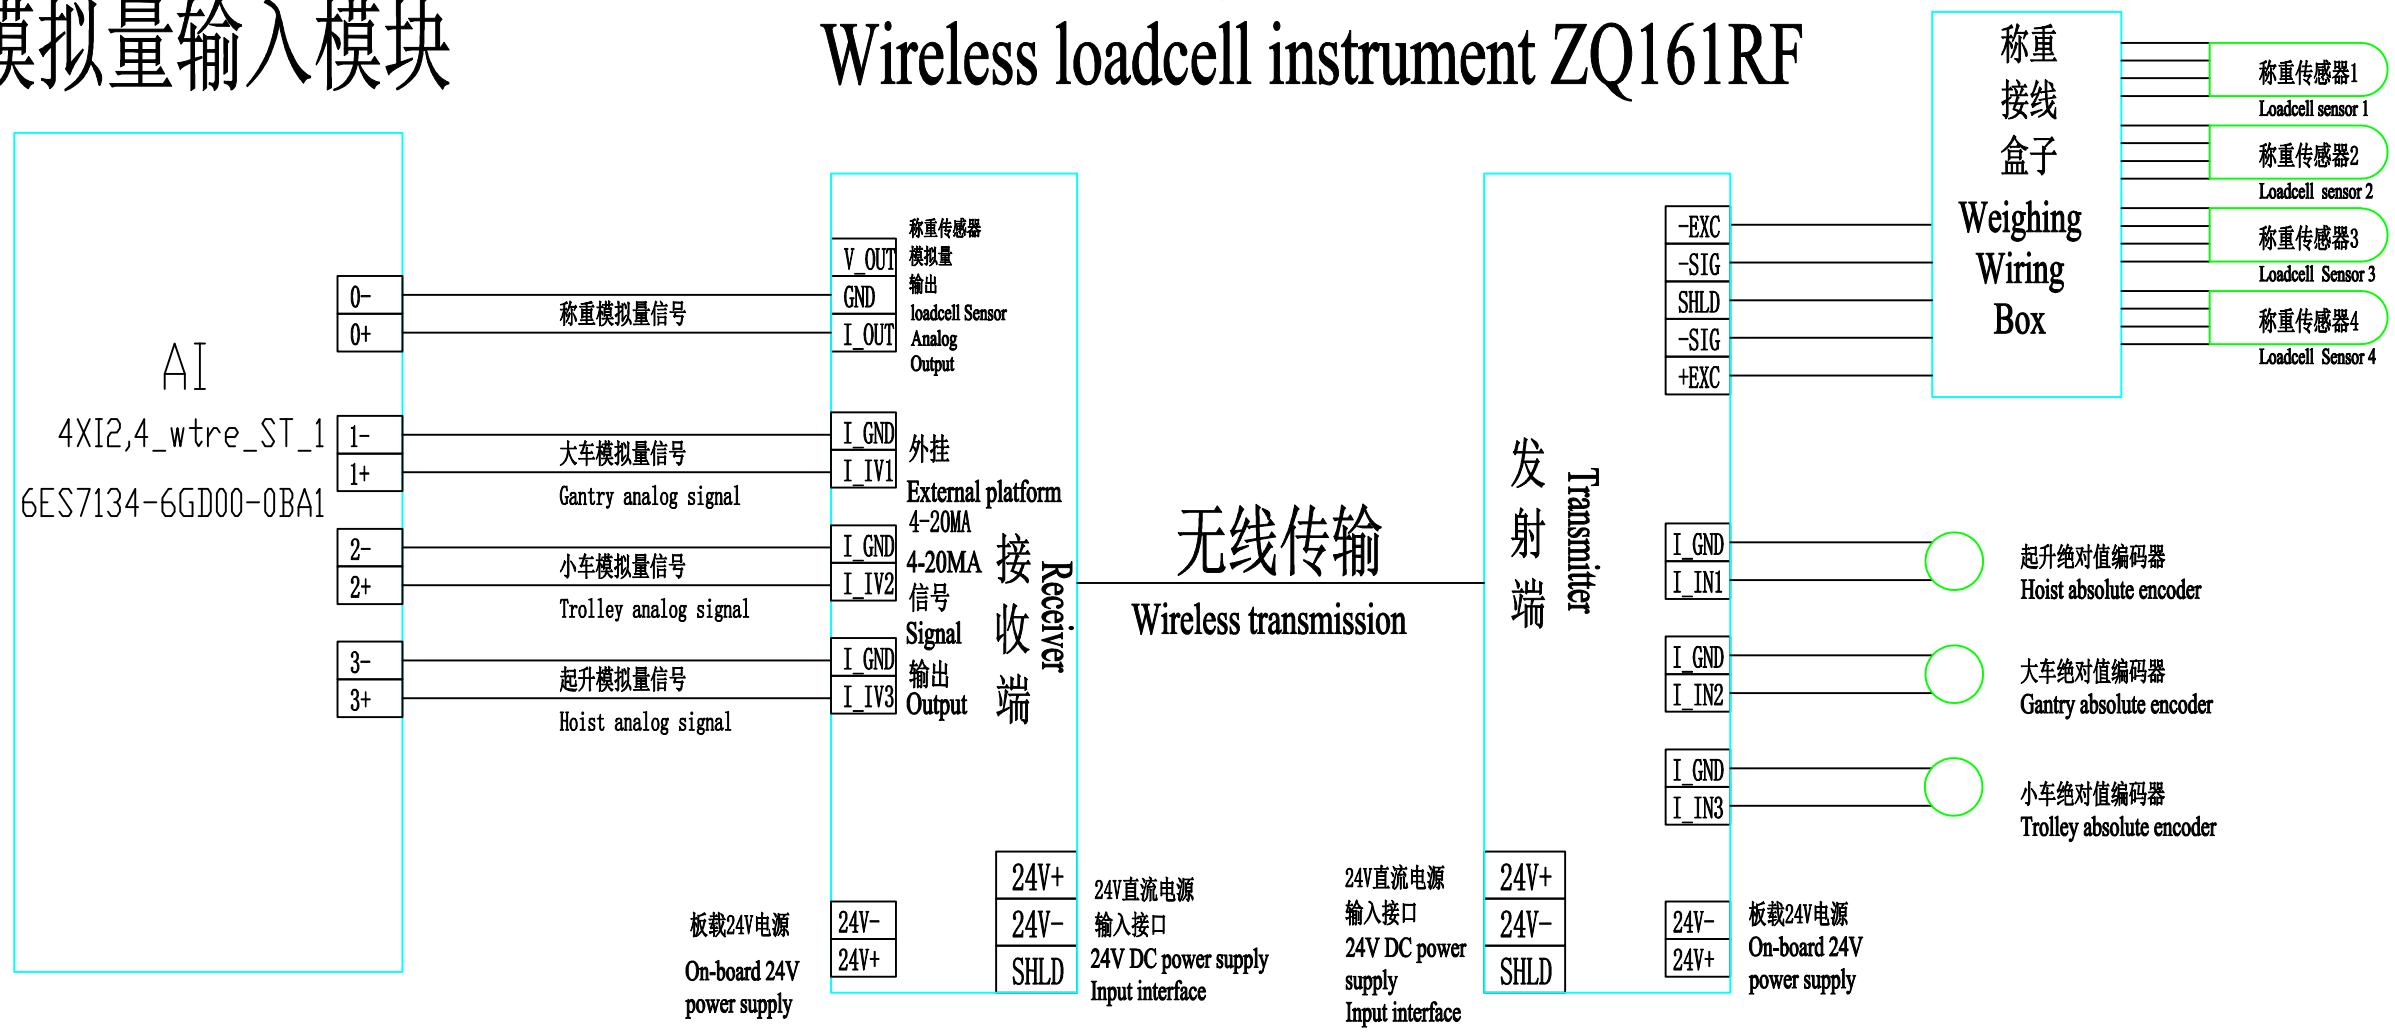

d					设计 Designed by	孙佳炀 Sun Jiawei			
c					审查 Reviewed by	董晨 Dong Chen			
b					主管设计 Chief Designer	石振 Shi Zhen			
a									
标记 Mark	处数 Nos.	更改文件号 Changed File No.	签字 Signature						

项目 Item	城市生活垃圾焚烧发电厂 垃圾抓斗桥式起重机 Municipal solid waste incineration power plant Waste grab bridge crane
	18t 37.1m A8

浙江浙起机械有限公司
Zhejiang Zheqi Machinery Co., Ltd.
地址：浙江省金华市金东区岭下朱工业区
Add: Lingxiazhu Industrial Zone, Jindong District, Jinhua City, Zhejiang Province

名称 Description	称重和编码器 图纸 Encoder and Loadcell Diagram	图号 DWG No.	QZL/0101-D
质量 Quality		比例 Scale	
		张数 Sheet	1
		第张 Next Page	本张 This page 1
		张次 Sheet of	1

图纸总张次 Total sheet	**
借(通)用件登记 Borrowed (General) Parts Registration	
描 Traced by 图	
描 Checked by 校	
旧底图总号 General No. of Old Traced Drawing	
底图总号 Base Drawing Total No.	
签字 Signature	
日期 Date	